Caderno de marcenaria

Projeto executivo para orçamento · cozinha, área de serviço e guarda-roupa da suíte

Objetivo. Reunir tudo o que um marceneiro precisa para orçar exatamente os mesmos móveis: medidas de cada módulo e de cada peça, materiais, fitas, ferragens, vistas, cortes e imagens 3D. Todas as medidas em **milímetros**. Revisão 00 de 13/11/2026. 28 pranchas em A3 e uma planilha de quantitativos.

Origem das medidas: **P** cota escrita na planta da construtora · **E** estimada pela escala da planta — conferir no local · **A** aparelho com medida típica — conferir o modelo · **T** proposta técnica do interior — a aprovar · **sem marca** medida do móvel no 3D aprovado

Escopo, em lotes

A1	Armários de baixo da parede A (M1 a M5) e rodapé
A2	Torre da geladeira (painel lateral + armário superior)
A3	Aéreos (off-white, faixa verde, madeira clara e nicho do micro-ondas)
A4	Área de serviço (módulo do tanque)
B1	Guarda-roupa de portas de espelho + coluna
B2	Guarda-roupa de portas cinza + canto
C1	Armário-ponte sobre a cama *(opcional)*
C2	Painel lateral da ponte *(opcional)*
C3	Cabeceira em painel *(opcional)*
C4	Criados suspensos (2) *(opcional)*

Leia antes de orçar

- Não houve medição no local: o **pé-direito (2600 mm) é estimado** e a medição técnica é obrigatória antes de fabricar.
- Os **modelos dos aparelhos não foram informados**: os nichos usam medidas típicas (prancha C-06).
- O **interior do guarda-roupa é proposta**, ainda a aprovar pelo cliente (marca **T**).
- Padrões de MDF e ferragens estão especificados por função e cor, **sem marca**: informar o que será usado.
- Pedras, cubas, aparelhos e instalações **não entram** neste orçamento.
- Preço **por lote**, no quadro da prancha Q-02. Pendências na P-01.



Cozinha — parede A (modelo 3D)



Suíte — guarda-roupa em L (modelo 3D)

Índice das pranchas

Folha	Cód.	Prancha
2	**N-01**	Notas gerais, sistema construtivo e materiais
3	**C-01**	Cozinha · planta e quadro de módulos
4	**C-02**	Cozinha · elevação A — vista externa
5	**C-03**	Cozinha · elevação A — vista interna
6	**C-04**	Cozinha · cortes transversais
7	**C-05**	Cozinha · área de serviço e canto do L
8	**C-06**	Cozinha · aparelhos, pontos de instalação e detalhe dos aéreos
9	**C-07**	Cozinha · módulos M1 e M2
10	**C-08**	Cozinha · módulos M3 e M4
11	**C-09**	Cozinha · módulos M5 e T1
12	**C-10**	Cozinha · módulos AG e NM
13	**C-11**	Cozinha · módulos AS e AM
14	**C-12**	Cozinha · painel, faixa verde e rodapé
15	**C-13**	Cozinha · imagens 3D
16	**G-01**	Suíte · planta e quadro de módulos
17	**G-02**	Suíte · elevação A — vista externa
18	**G-03**	Suíte · elevação A — vista interna
19	**G-04**	Suíte · elevação B — vistas externa e interna
20	**G-05**	Suíte · cortes
21	**G-06**	Suíte · módulos G2 e CO
22	**G-07**	Suíte · módulo G4 (portas cinza + canto)
23	**G-08**	Suíte · complementos: AP, CR, PJ e CB
24	**G-09**	Suíte · painel lateral e cabeceira
25	**G-10**	Suíte · imagens 3D
26	**Q-01**	Quantitativos · materiais, fitas e ferragens
27	**Q-02**	Quadro para orçamento (preencher e devolver)
28	**P-01**	Pendências, medidas a conferir e decisões em aberto

Códigos dos módulos

Cozinha: M1 a M5 armários de baixo · RA rodapé · PG painel da geladeira · AG armário sobre a geladeira · AS aéreo superior · FV faixa verde · AM aéreo de madeira · NM nicho do micro-ondas · T1 módulo do tanque.
Suíte: G2 guarda-roupa de espelho · G4 guarda-roupa de portas cinza + canto · CO coluna · AP armário-ponte · PJ painel lateral · CB cabeceira · CR1 e CR2 criados.

Totais de referência

21 módulos · 247 peças de MDF · 85,1 m² de chapa (área líquida) · 253 m de fita de borda · 25 portas e 10 gavetas.

DOCUMENTO	PRANCHA	ESCALA	UNIDADE	REVISÃO · DATA	FOLHA
Caderno de marcenaria Projeto executivo para orçamento	**CAPA — Capa, escopo e índice**	—	mm	00 · 13/11/2026	1/28

Sistema construtivo de referência

Padrão único para que todos orcem a mesma coisa. Quem trabalhar com outro sistema (por exemplo, caixa de 18 mm) deve cotar este como base e a alternativa em separado.

Caixas	MDF BP 15 mm branco TX, 2 faces. Laterais inteiras; base e tampo entre as laterais; união por cavilha e minifix (ou parafuso estrutural oculto).
Frentes e peças aparentes	MDF BP 18 mm, 2 faces, no padrão indicado em cada módulo (portas, frentes de gaveta, painéis, molduras, réguas e rodapés).
Fundos	MDF BP 6 mm branco, sobrepostos e parafusados (ou em canal), 2 mm menores que a caixa de cada lado.
Prateleiras	15 mm; 18 mm quando o vão passa de 800 mm ou recebe aparelho. Reguláveis: 4 pinos, 1 mm de folga lateral e 20 mm de recuo na frente.
Gavetas	Caixa em MDF 15 mm branco (2 laterais, contrafrente e traseira) e fundo de 6 mm. Corrediça telescópica: 13 mm de cada lado.
Folgas	3 mm entre frentes; 3 mm no topo e na base das frentes; 2 mm de batente entre a frente e a caixa.
Fitas de borda	PVC 1 mm na cor do painel em todas as bordas das frentes e peças aparentes; PVC 0,45 mm nas bordas visíveis das caixas. Nas listas: C = borda do comprimento, L = borda da largura.
Rodapés	Cozinha: 100 mm, recuado 60 mm, removível, sobre pés reguláveis. Guarda-roupa: 80 mm, recuado 60 mm na frente.
Painéis engrossados	30 mm = 2 chapas de 15 mm coladas (painel da geladeira e painel da ponte).
Réguas de ajuste	Parede e teto fora de prumo: prever réguas de arremate no mesmo padrão, definidas na medição e incluídas no preço.
Fixação	Aéreos em suporte regulável com bucha adequada à alvenaria; armário-ponte com fixação reforçada.
Montagem	No local, incluída. Portas acima de 2.000 mm com tensor.

Padrões de acabamento

As cores abaixo são as do 3D aprovado. Não há marca definida: cada marceneiro informa fabricante, linha e nome do padrão que propõe e apresenta amostra.

Cor	Padrão	Onde
	Branco TX MDF BP branco texturizado, 2 faces	Interior das caixas, prateleiras, gavetas e fundos
	Verde sálvia MDF BP verde sálvia fosco, 2 faces	Frentes dos armários de baixo da cozinha, faixa entre os aéreos, rodapé
	Off-white MDF BP off-white fosco, 2 faces	Aéreo superior, armário e painel da torre da geladeira
	Madeira clara MDF BP madeirado claro (tom natural/mel, com veio), 2 faces	Aéreo inferior e nicho do micro-ondas
	Carvalho claro MDF BP madeirado carvalho claro, 2 faces	Suíte: coluna, molduras, lateral aparente, armário-ponte, cabeceira, painel e criados
	Cinza MDF BP cinza médio fosco, 2 faces	Portas do guarda-roupa G4 e rodapés do guarda-roupa
	Espelho Prata 3 mm, bordas lapidadas, colado	Portas do G2
	Puxador cava Perfil de alumínio escuro fosco	Topo das frentes de baixo da cozinha

Fora deste orçamento (outros fornecedores)

- Bancadas de quartzo, frontões de granilite e revestimento do shaft (marmoraria).
- Cubas, torneiras e eletrodomésticos.
- Pontos elétricos, hidráulicos e de gás; fitas de LED do teto.
- Banheiro, quarto 2, rack e demais móveis: não fazem parte deste caderno.

Regras para o orçamento

- **Preço por lote**, separado: A1 a A4 (cozinha), B1 e B2 (guarda-roupa) e, como opcionais, C1 a C4 (complementos da suíte). Usar o quadro da prancha Q-02.
- **Informar** fabricante e linha do MDF e das ferragens, prazo de entrega e de montagem, garantia, validade da proposta e forma de pagamento.
- **Incluir no preço**: medição técnica, projeto de fabricação, todas as ferragens listadas, réguas de ajuste, recortes para instalações, transporte, montagem e limpeza.
- **Itens opcionais** (perfil de LED sob o aéreo, organizador de talheres, alternativas de abertura): cotar em linha separada.
- **Alternativas técnicas** do marceneiro são bem-vindas, sempre como opção à parte, sem mexer no preço-base.
- **Lista de peças é de referência**: serve para dimensionar material e mão de obra. O plano de corte definitivo é do marceneiro, depois da medição no local.
- **Divergência** entre este caderno e a medição: avisar antes de fabricar.


Medição técnica antes da fabricação

As cotas marcadas **P** vêm da planta da construtora; as marcadas **E** foram lidas pela escala da imagem. O **pé-direito (2600 mm) é estimado** e define a altura de tudo o que vai até o teto. Nenhuma peça deve ser cortada sem a medição no local. Pendências completas na prancha P-01.


Correspondência com o 3D

Largura, altura, profundidade e posição de cada módulo saem diretamente do modelo 3D aprovado (base 2026-11-13.4); as vistas, os cortes e as listas são gerados das mesmas peças. O interior dos armários não aparece no 3D: é proposta técnica, marcada **T**.

Detalhe-tipo — armário de baixo (corte, 1:10)

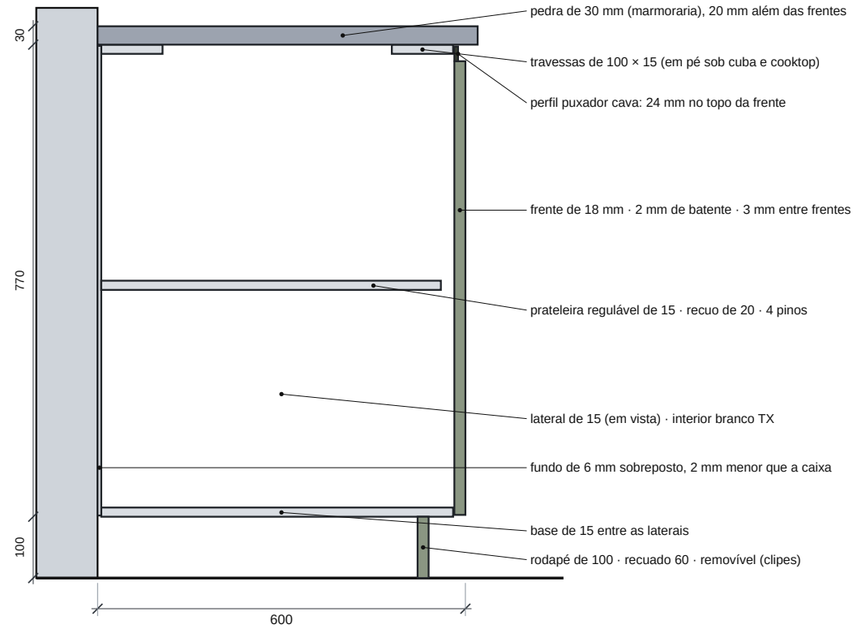

Origem das medidas: **P** cota escrita na planta da construtora · **E** estimada pela escala da planta — conferir no local · **A** aparelho com medida típica — conferir o modelo · **T** proposta técnica do interior — a aprovar · **sem marca** medida do móvel no 3D aprovado

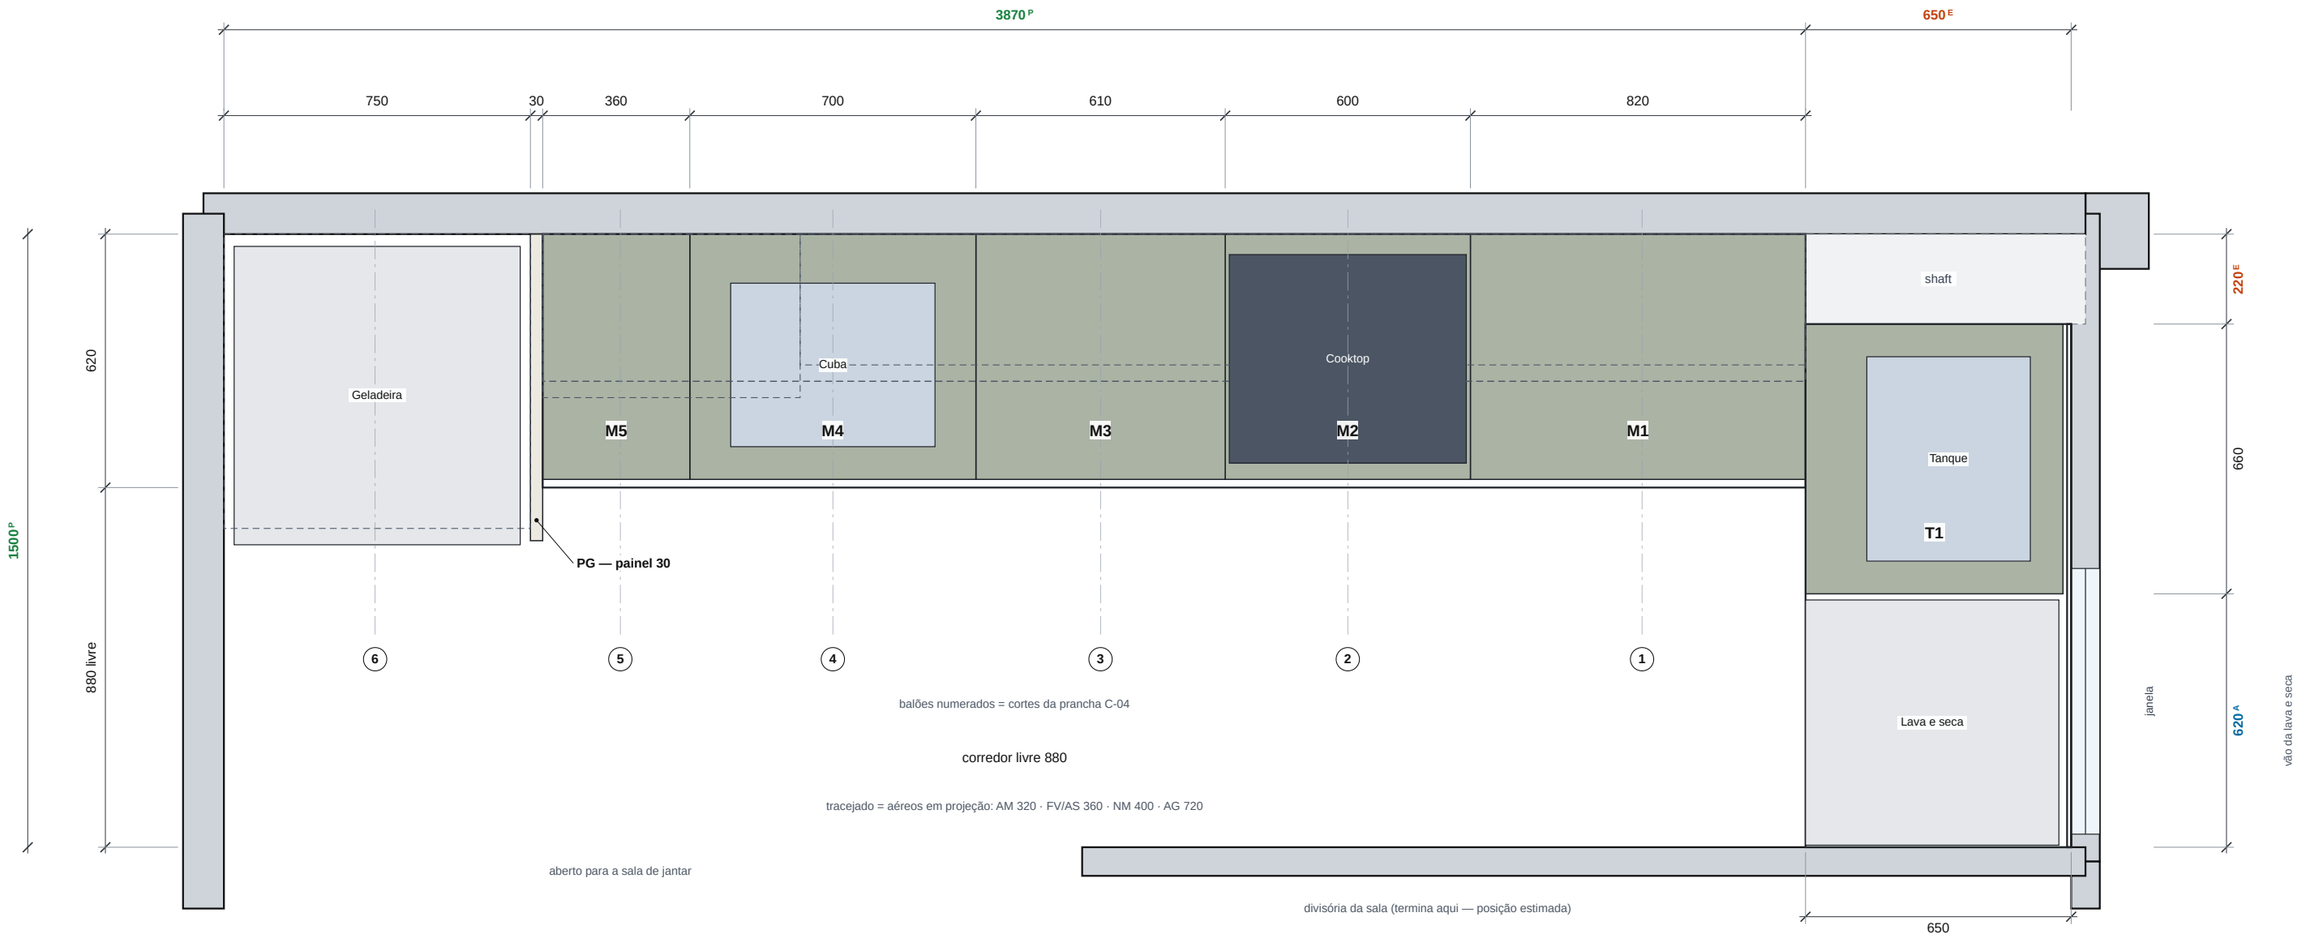


Cód.	Módulo	Lote	L × A × P	Base a	Frentes e acabamento	Peças	MDF m²
M1	Gaveteiro do canto	A1	820 × 870 × 600	piso	3 gavetas verde sálvia com puxador cava no topo de cada frente; a de baixo é a mais alta (proporção do 3D).	24	5,11
M2	Módulo do forno e cooktop	A1	600 × 870 × 600	piso	Forno de embutir à vista; régua fixa de 54 mm embaixo e frente fixa de 114 mm em cima (com a linha do cava alinhada aos vizinhos).	7	1,42
M3	Módulo da lava-louças compacta	A1	610 × 870 × 600	piso	Lava-louças à vista em nicho elevado; gaveta baixa embaixo (frente lisa de 154 mm, como no 3D).	12	2,65
M4	Armário da pia	A1	700 × 870 × 600	piso	2 portas verde sálvia com puxador cava.	8	2,45
M5	Armário de 1 porta	A1	360 × 870 × 600	piso	1 porta verde sálvia com puxador cava.	8	1,86
RA	Rodapé da bancada (parede A)	A1	3090 × 100 × 18	piso	Rodapé recuado 60 mm do plano das frentes, altura 100 mm, do canto ao painel da geladeira.	2	0,31
PG	Painel lateral da torre da geladeira	A2	30 × 2600 × 750	piso	Painel off-white de 30 mm (engrossado), do piso ao teto, 750 mm de profundidade.	2	3,90
AG	Armário sobre a geladeira	A2	750 × 620 × 720	1980	2 portas off-white lisas, sem puxador, até o teto.	8	3,26
AS	Aéreo superior off-white	A3	3090 × 620 × 360	1980	4 portas off-white lisas de 769,5 × 614 mm, sem puxador, até o teto.	20	7,97
FV	Faixa verde entre os aéreos	A3	3090 × 80 × 360	1900	Faixa verde sálvia de 80 mm de altura em toda a extensão dos aéreos, no mesmo plano do aéreo superior.	5	0,46
AM	Aéreo inferior em madeira clara	A3	2460 × 350 × 320	1550	5 portas em madeira clara de 489 × 344 mm, sem puxador. Recuado 40 mm em relação à faixa verde.	18	3,79
NM	Nicho do micro-ondas	A3	630 × 350 × 400	1550	Nicho aberto em madeira clara, 18 mm, 40 mm mais fundo que a faixa verde e 80 mm mais fundo que o aéreo de madeira.	5	0,96
T1	Módulo do tanque (canto cego)	A4	660 × 870 × 630	piso	Do módulo de 660 mm só 280 mm ficam à vista (o resto fica atrás do gaveteiro M1): régua de canto de 40 mm + 1 porta de 237 mm com puxador cava.	9	2,17

Origem das medidas: **P** cota escrita na planta da construtora · **E** estimada pela escala da planta — conferir no local · **A** aparelho com medida típica — conferir o modelo · **T** proposta técnica do interior — a aprovar · **sem marca** medida do móvel no 3D aprovado

Elevação A — vista externa

Parede da bancada, vista do corredor. Triângulos tracejados: abertura das portas (o vértice fica do lado das dobradiças).

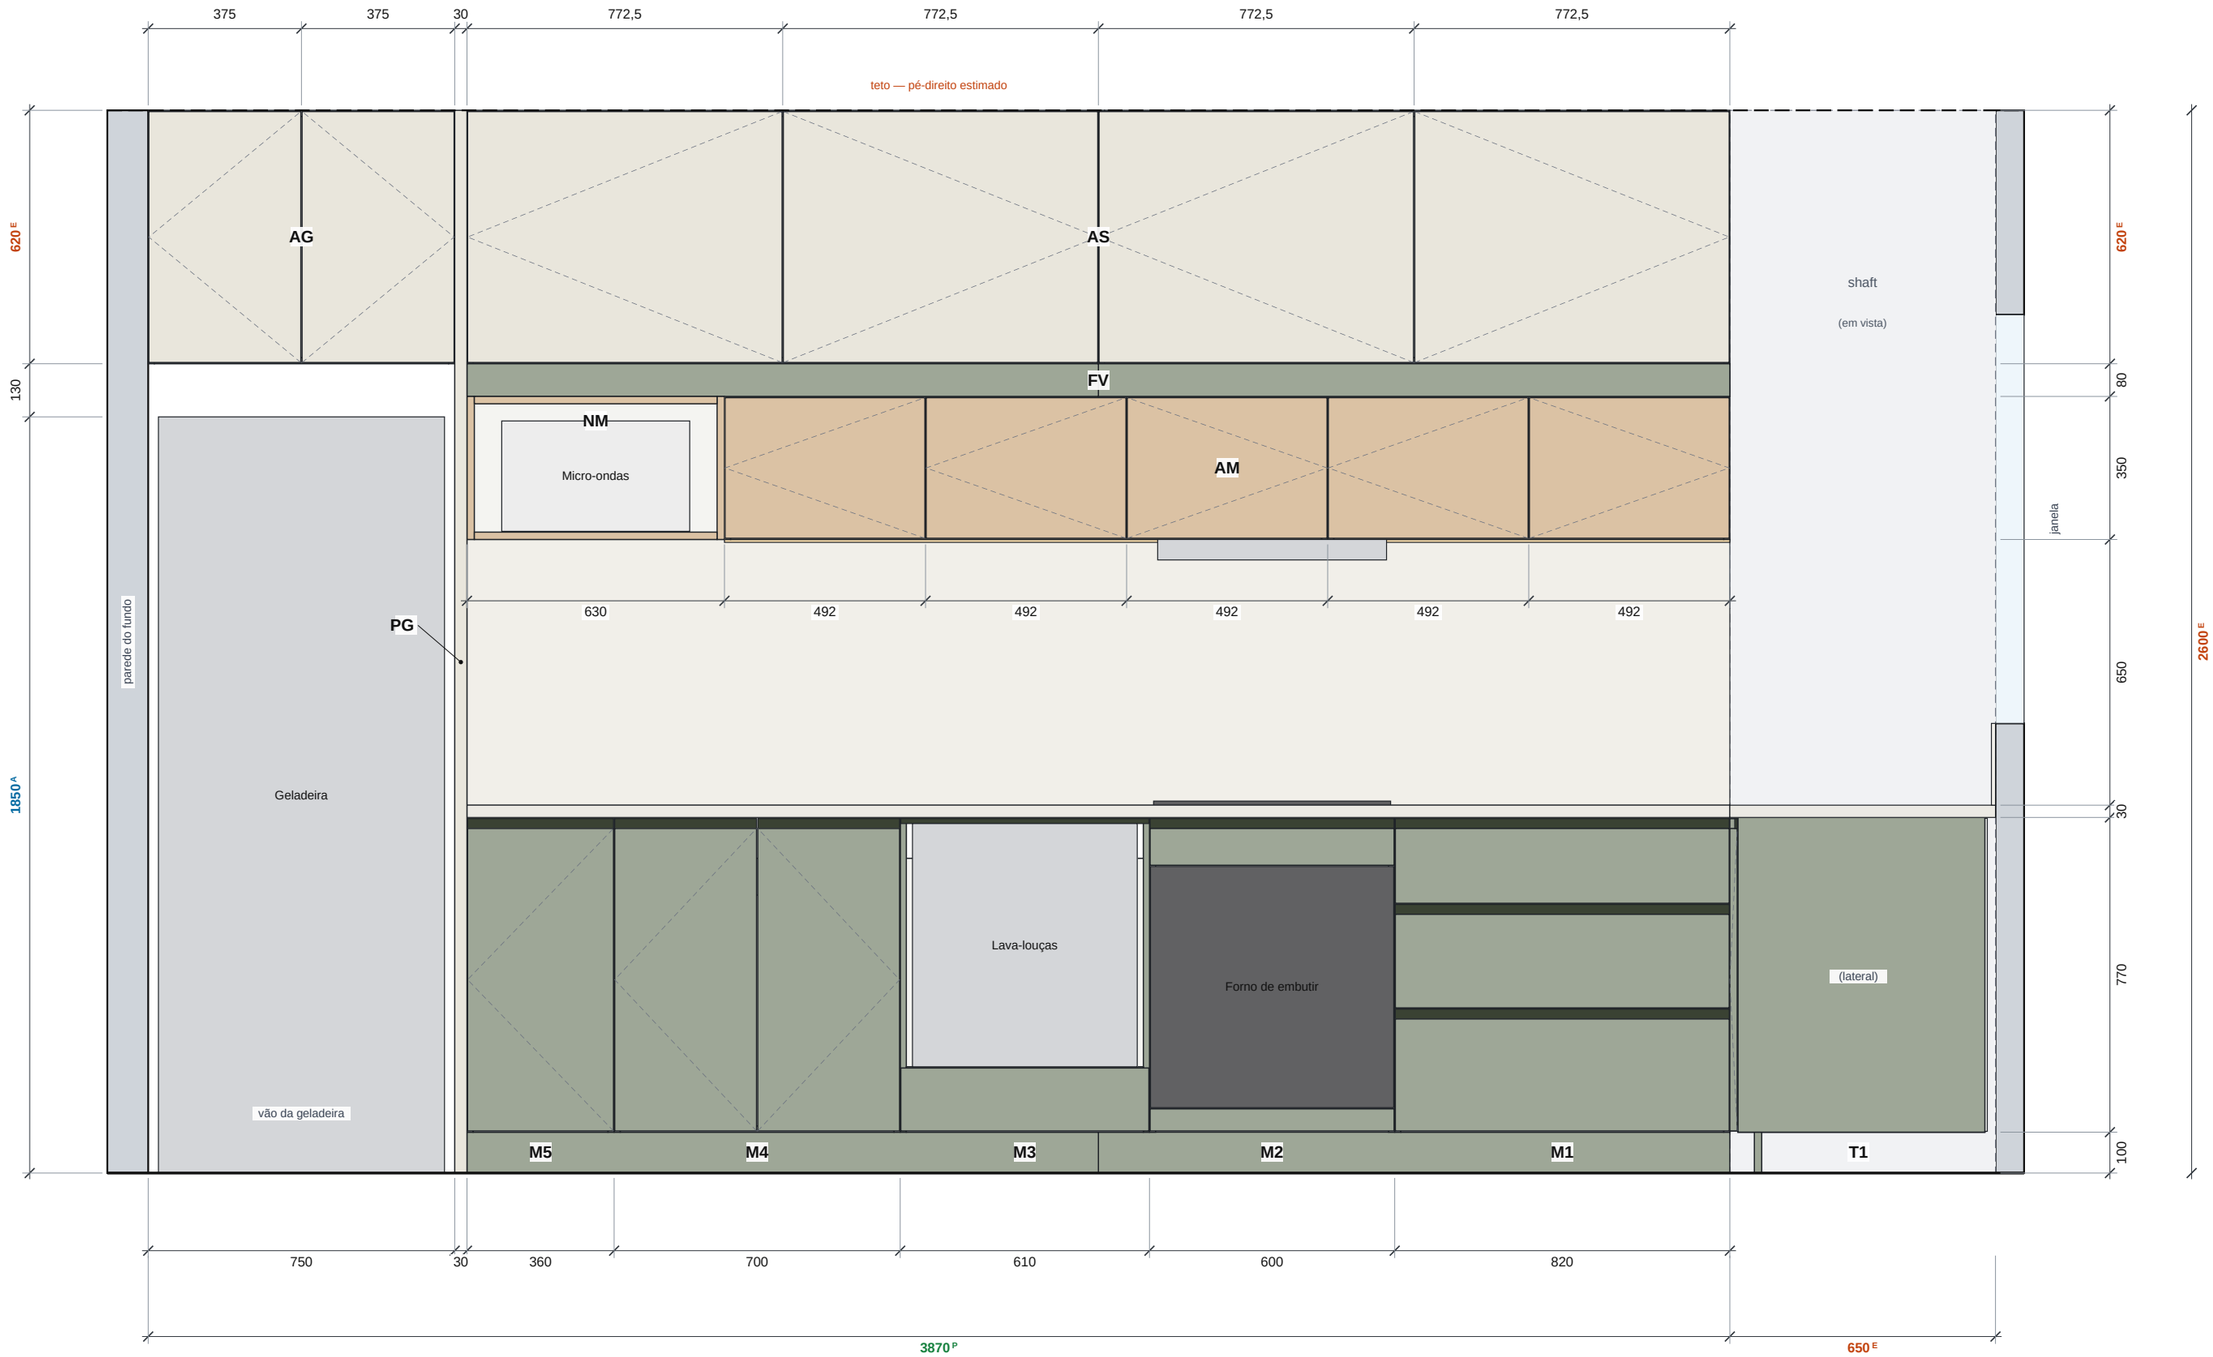


DOCUMENTO	PRANCHA	ESCALA	UNIDADE	REVISÃO · DATA	FOLHA
Caderno de marcenaria Projeto executivo para orçamento	**C-02 — Cozinha · elevação A — vista externa**	**1:15**	**mm**	**00 · 13/11/2026**	**4/28**

Origem das medidas: **P** cota escrita na planta da construtora · **E** estimada pela escala da planta — conferir no local · **A** aparelho com medida típica — conferir o modelo · **T** proposta técnica do interior — a aprovar · **sem marca** medida do móvel no 3D aprovado

Elevação A — vista interna (sem portas e frentes)

Caixas, divisórias, prateleiras e gavetas. Aparelhos em tracejado, com medidas típicas (ver prancha C-06).

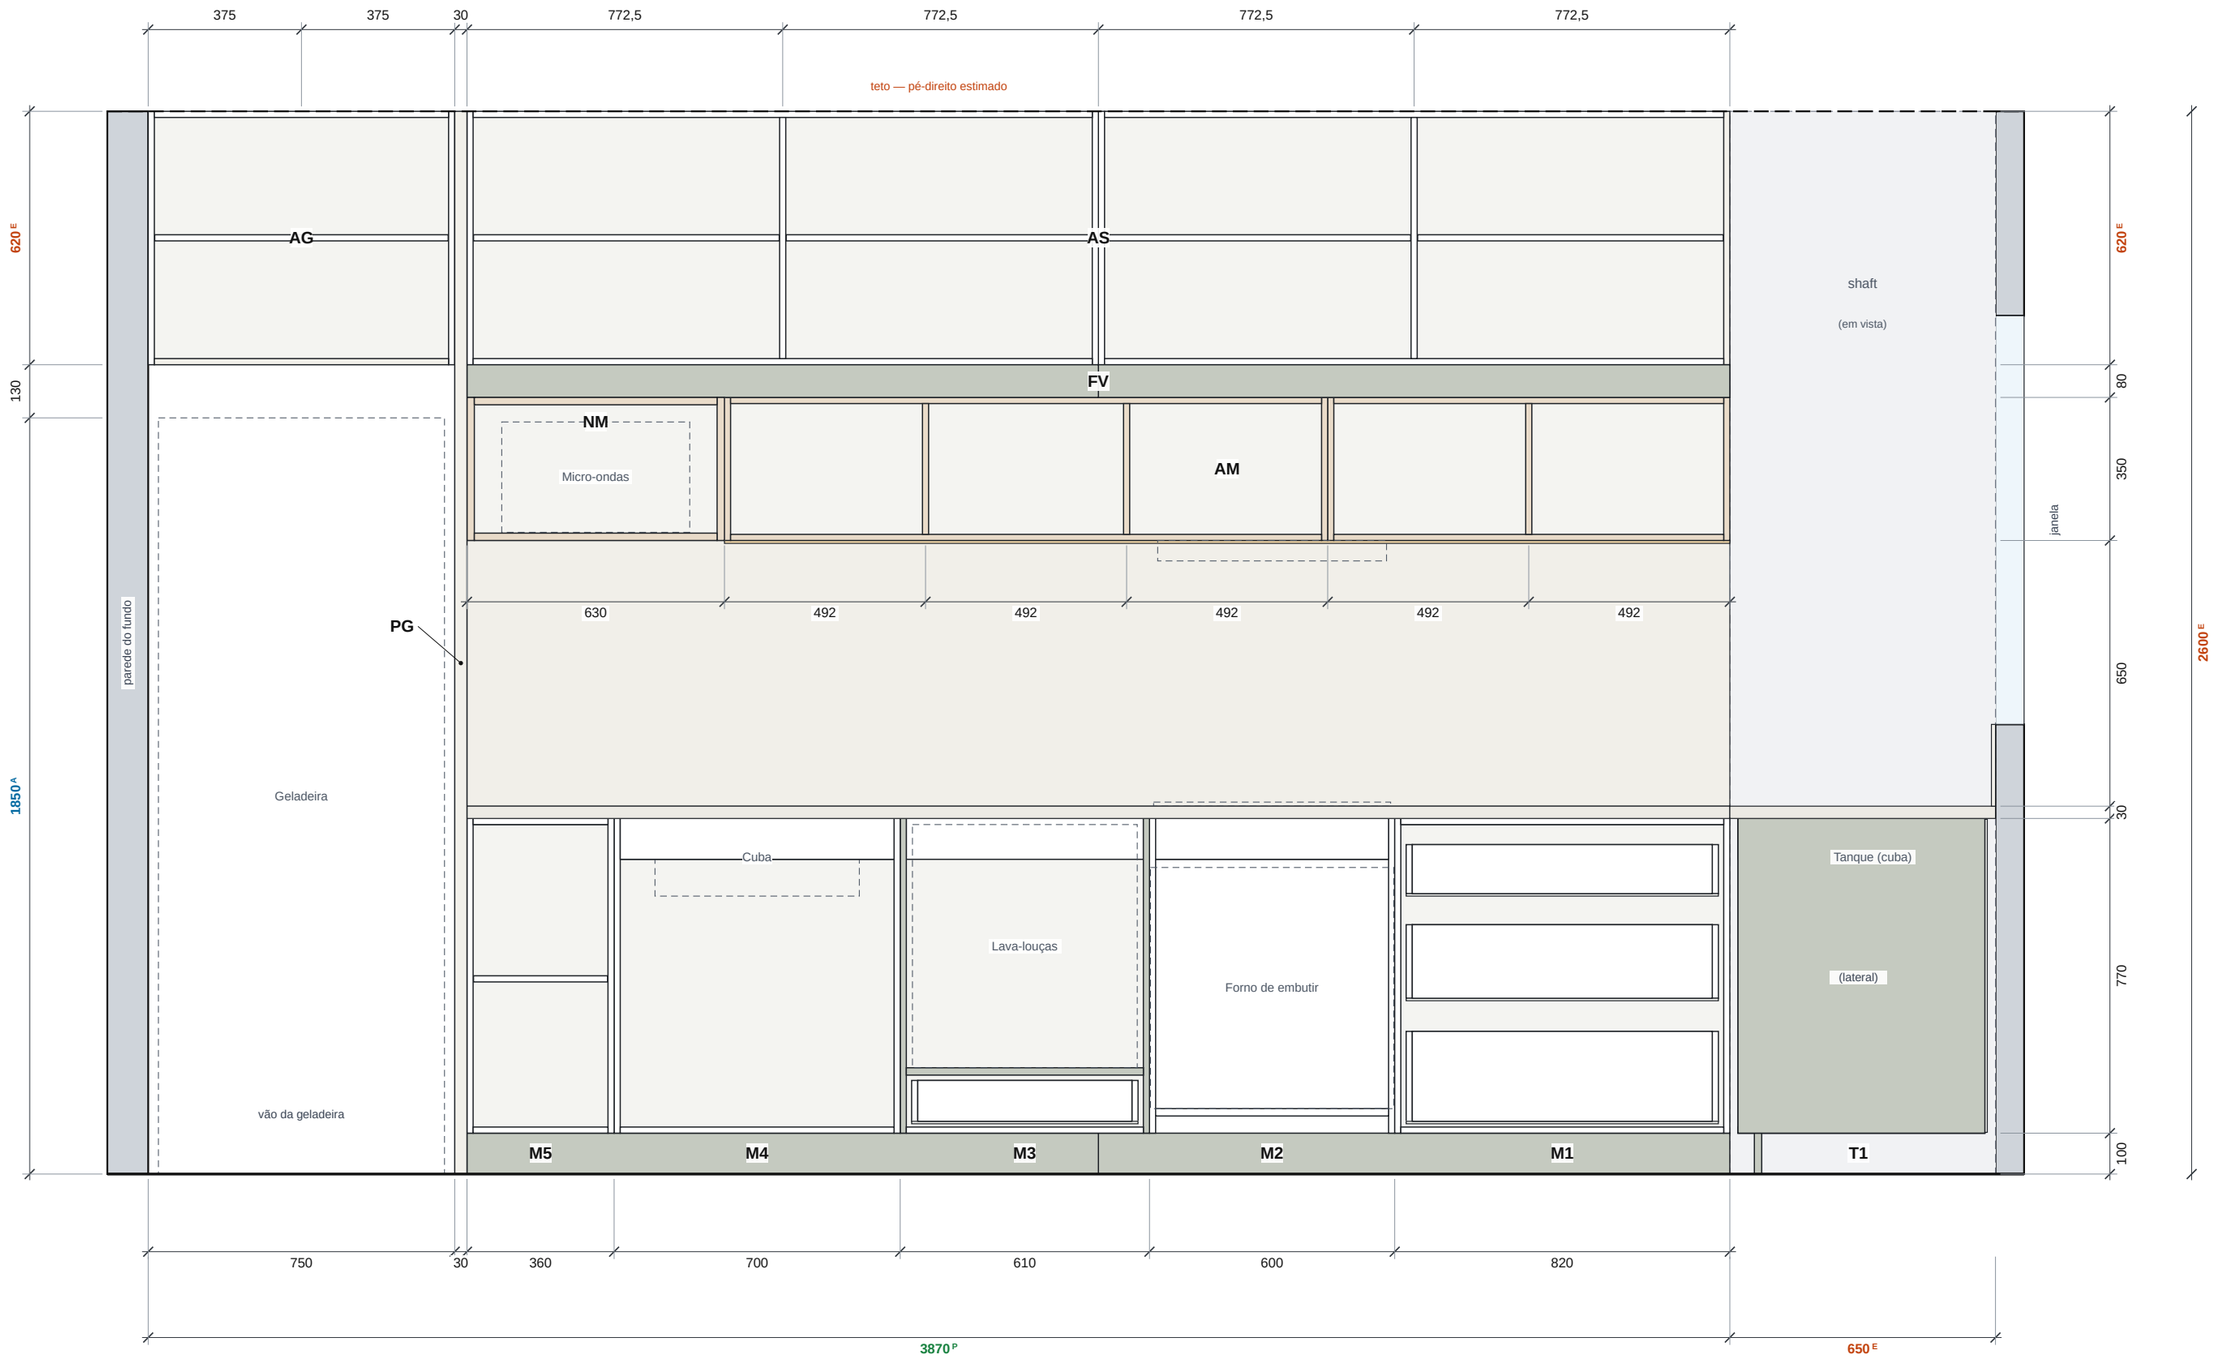

DOCUMENTO	PRANCHA	ESCALA	UNIDADE	REVISÃO · DATA	FOLHA
Caderno de marcenaria Projeto executivo para orçamento	**C-03 — Cozinha · elevação A — vista interna**	**1:15**	**mm**	**00 · 13/11/2026**	**5/28**


Origem das medidas: **P** cota escrita na planta da construtora · **E** estimada pela escala da planta — conferir no local · **A** aparelho com medida típica — conferir o modelo · **T** proposta técnica do interior — a aprovar · **sem marca** medida do móvel no 3D aprovado

Cortes transversais da parede A

Posições na planta (C-01): corte 1 a 400 mm do shaft · corte 2 a 1120 mm do shaft · corte 3 a 1725 mm do shaft · corte 4 a 2380 mm do shaft · corte 5 a 2900 mm do shaft · corte 6 a 3500 mm do shaft. Peças cortadas em cinza; o que fica atrás, em vista.


Corte 1

M1 · AM · FV · AS

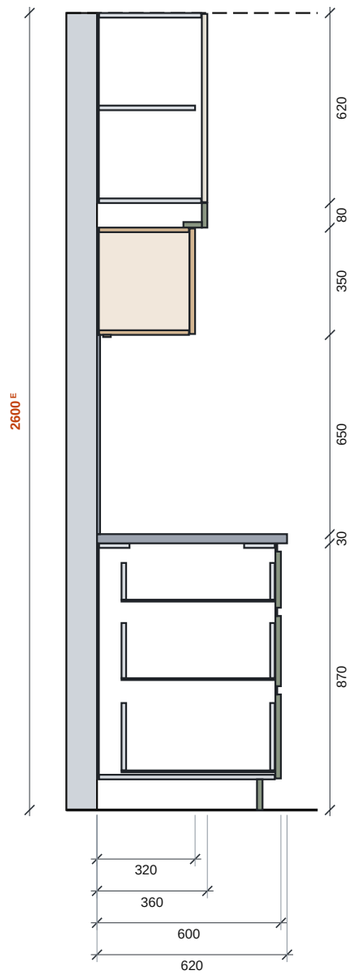


Corte 2

M2 · cooktop · depurador

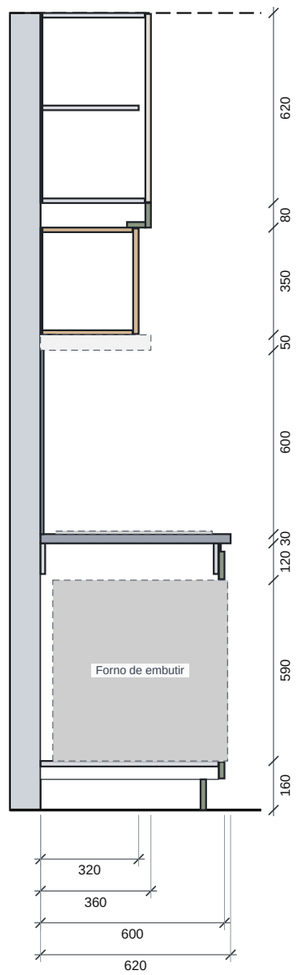


Corte 3

M3 · lava-louças

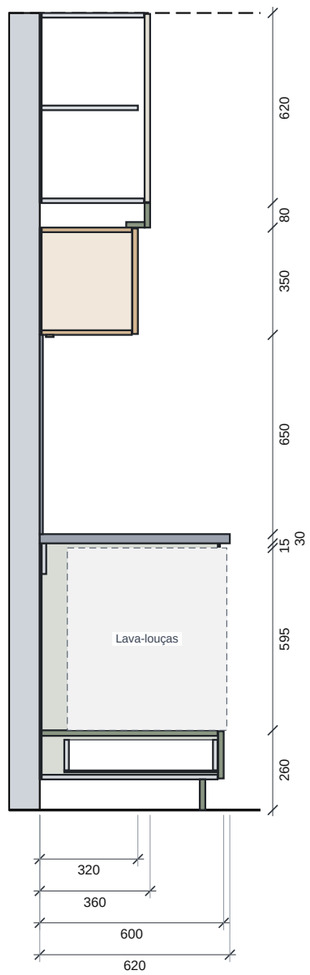


Corte 4

M4 · cuba

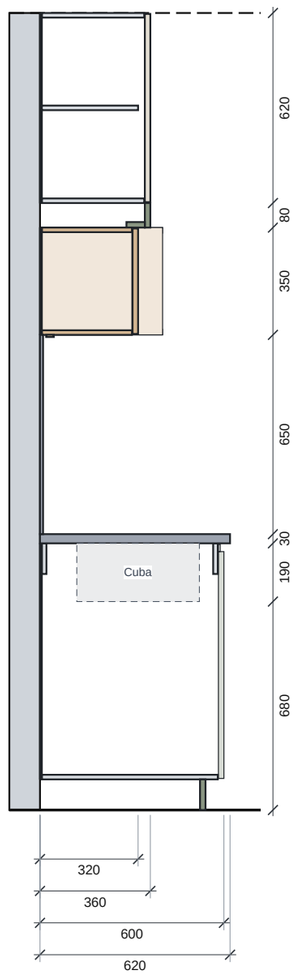


Corte 5

M5 · nicho do micro-ondas

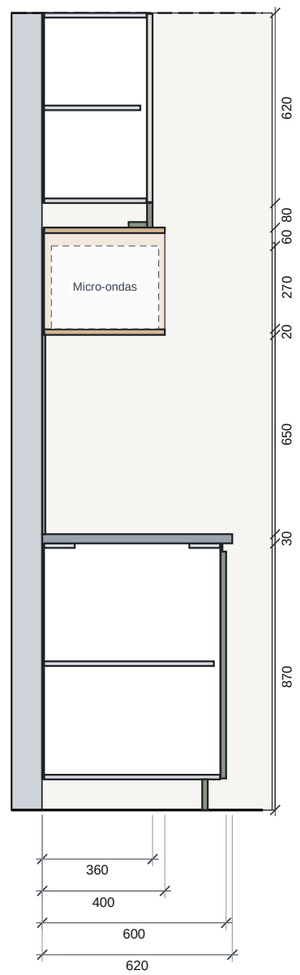

Corte 6


torre da geladeira · AG

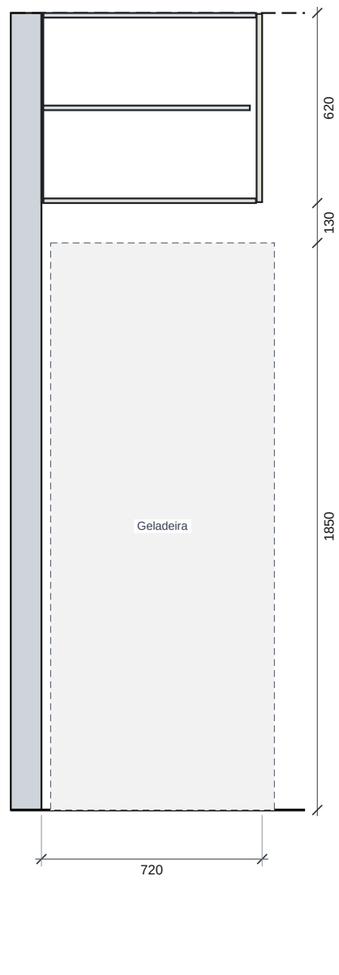


DOCUMENTO	PRANCHA	ESCALA	UNIDADE	REVISÃO · DATA	FOLHA
Caderno de marcenaria Projeto executivo para orçamento	**C-04 — Cozinha · cortes transversais**	**1:20**	**mm**	**00 · 13/11/2026**	**6/28**

Origem das medidas: **P** cota escrita na planta da construtora · **E** estimada pela escala da planta — conferir no local · **A** aparelho com medida típica — conferir o modelo · **T** proposta técnica do interior — a aprovar · **sem marca** medida do móvel no 3D aprovado


Elevação B — vista externa (com a parede A em perfil)

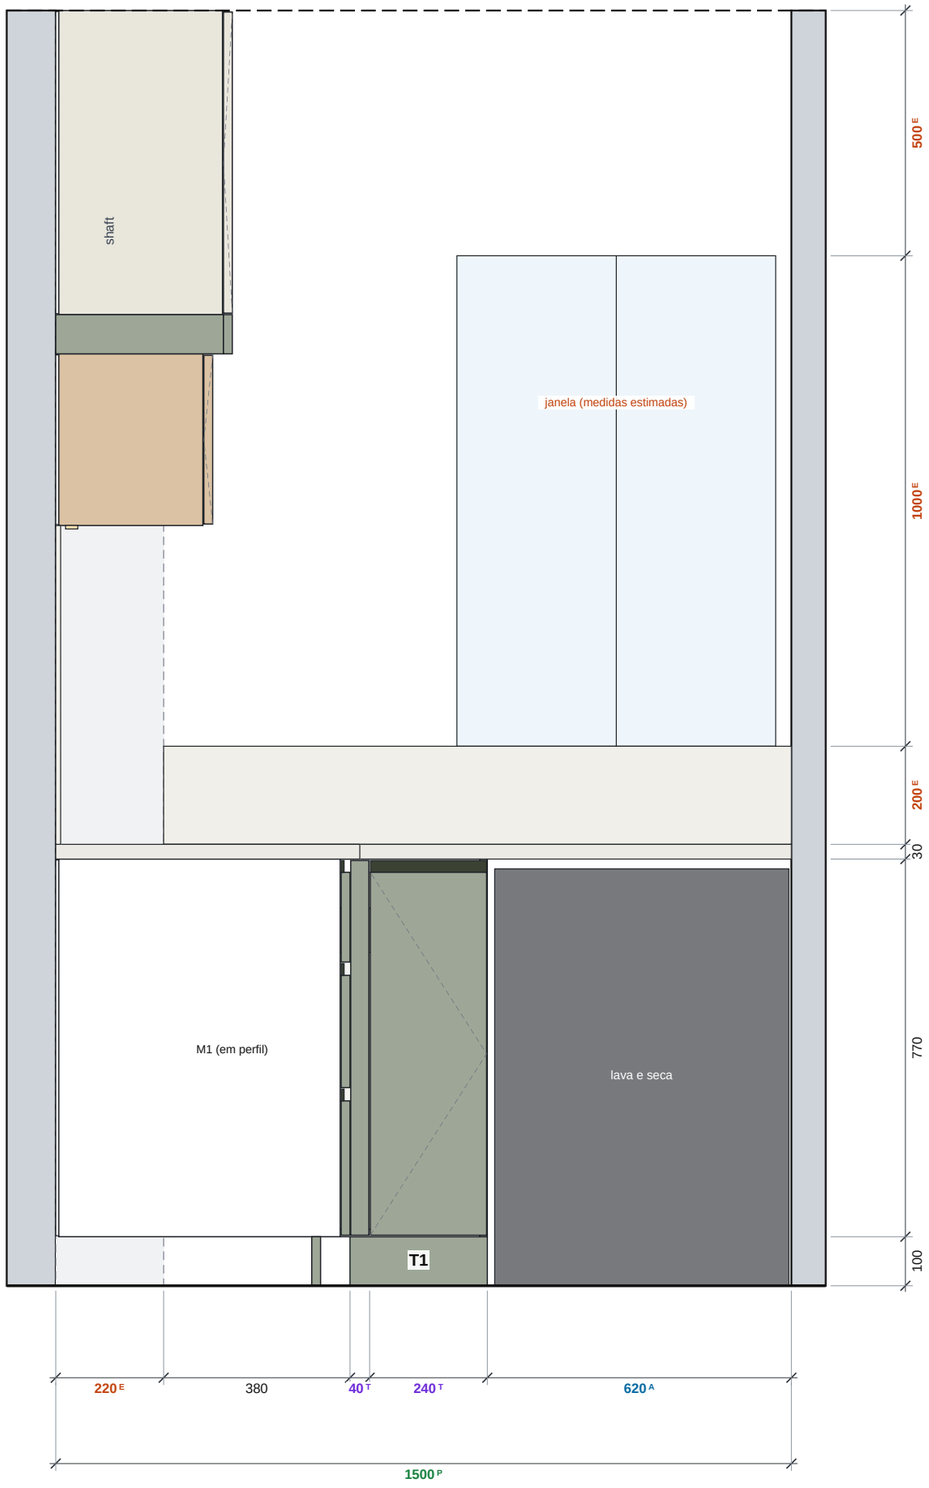

Corte 7

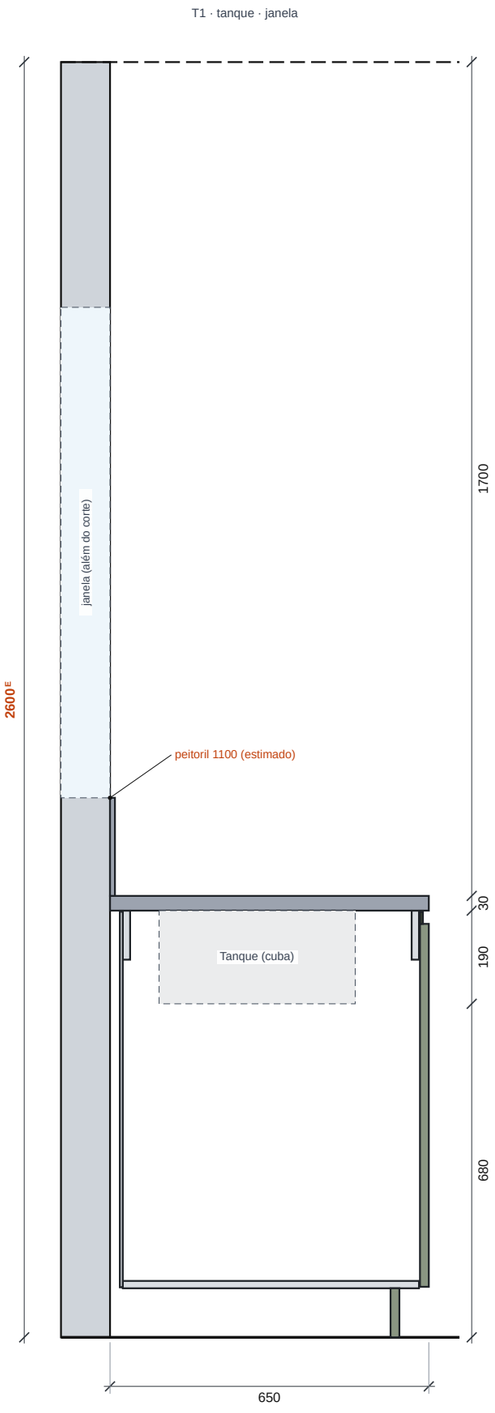

Detalhe do canto em planta

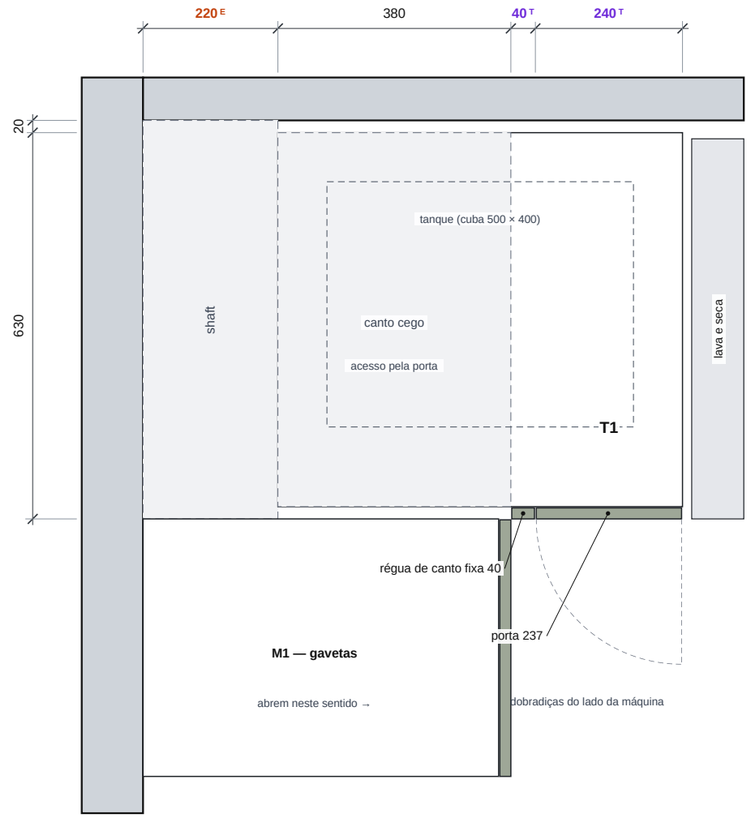

DOCUMENTO	PRANCHA	ESCALA	UNIDADE	REVISÃO · DATA	FOLHA
Caderno de marcenaria Projeto executivo para orçamento	**C-05 — Cozinha · área de serviço e canto do L**	**1:12,5 e 1:10**	**mm**	**00 · 13/11/2026**	**7/28**

Aparelhos e vãos previstos

Nenhum modelo foi informado: as medidas dos aparelhos são típicas de mercado. Informar marca e modelo antes de fechar os vãos.


Aparelho	Situação	Aparelho (L × A × P)	Vão previsto (L × A × P)	Onde	Atenção
Geladeira (freezer embaixo)	Já tem	700 × 1850 × 730 **A**	750 × 1980 × 750	Torre (PG + AG)	Folga lateral e abertura da porta junto à parede do fundo; ventilação pedida no manual.
Forno de embutir 60 cm	A comprar	595 × 590 × 570 **A**	570 × 590 × 580	M2	Nicho, ventilação e posição da tomada conforme o manual; modelo não definido.
Cooktop 4 bocas	A comprar	580 × 10 × 510 **A**	—	Sobre o M2 (recorte na pedra)	Recorte da pedra e distância ao forno conforme o manual.
Depurador slim 60 cm	A comprar	560 × 50 × 360 **A**	600 de altura livre	Sob o AM, sobre o cooktop	Ficam 600 mm livres entre o cooktop e o depurador: os manuais costumam pedir de 650 a 750 mm (mais para gás). Conferir antes de fechar a altura do aéreo.
Lava-louças compacta (8 serviços)	Já tem	550 × 595 × 520 **A**	580 × 595 × 574	M3 (nicho elevado)	Folga vertical zero com a medida típica; porta aberta avança ≈ 550 mm no corredor de 880 mm.
Micro-ondas	Já tem	460 × 270 × 350 **A**	594 × 314 × 394	NM (nicho aberto)	Ventilação lateral e superior conforme o manual.
Lava e seca (abertura frontal)	Já tem	600 × 850 × 620 **A**	620 × 870 × 650	Sob a pedra da janela, ao lado do T1	Mangueiras atrás pedem 50–80 mm: a máquina pode ficar para fora da pedra. Sob a pedra sobram ≈ 20 mm.

Pontos de instalação que a marcenaria precisa encontrar

A posição dos pontos existentes não consta na planta. A coluna "onde deve ficar" é a necessidade do projeto; confirmar com o eletricista e o encanador o que já existe.


Ponto	Onde deve ficar	Para quê
Geladeira (freezer embaixo)	Torre (PG + AG)	Tomada acessível atrás ou acima do aparelho
Forno de embutir 60 cm	M2	Tomada dedicada fora do nicho (potência conforme o modelo)
Cooktop 4 bocas	Sobre o M2 (recorte na pedra)	Gás (registro acessível) ou circuito elétrico dedicado — tipo não definido
Depurador slim 60 cm	Sob o AM, sobre o cooktop	Tomada dentro do aéreo de madeira
Lava-louças compacta (8 serviços)	M3 (nicho elevado)	Água e esgoto pelo módulo da pia (M4); tomada no M4
Micro-ondas	NM (nicho aberto)	Tomada no fundo do nicho
Lava e seca (abertura frontal)	Sob a pedra da janela, ao lado do T1	Água, esgoto e tomada na parede (lateral ou da janela)
Pia	Dentro do M4, abaixo da cuba	Água fria e esgoto; recorte no fundo do módulo
Tanque	Dentro do T1 ou na parede da janela	Água fria e esgoto; no decorado a torneira sai da parede
Fita de LED sob o aéreo	Fonte no vazio da faixa verde (FV)	Ponto de energia com interruptor
Tomadas de bancada	No frontão, entre 900 e 1.550 mm	Recortes na pedra (marmoraria); não interferem nos armários

Detalhe — encontro dos aéreos (corte, 1:5)

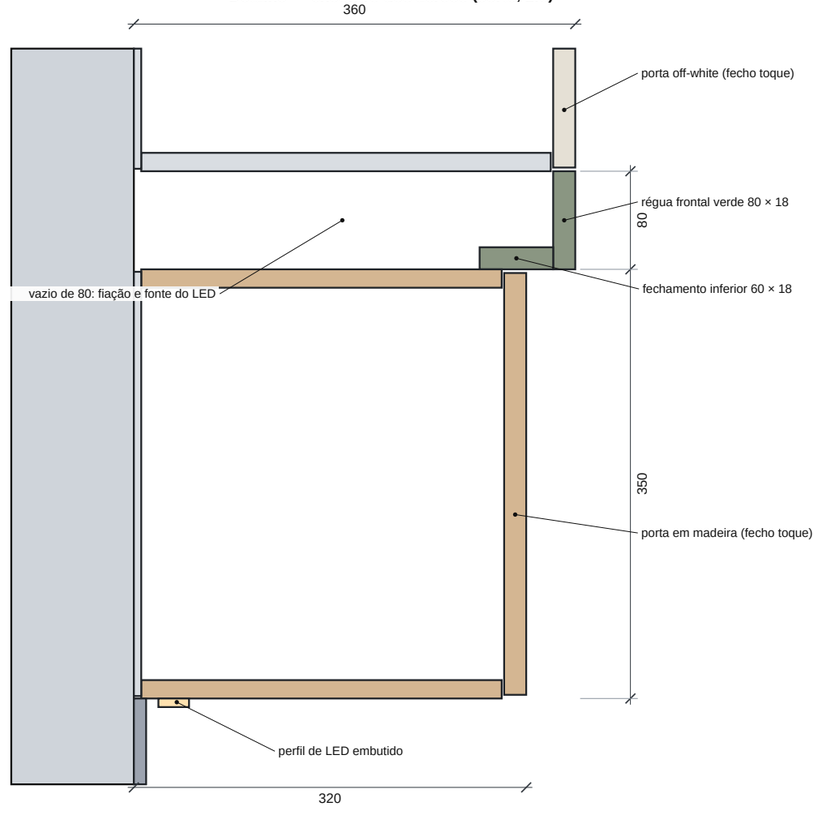

M1 Gaveteiro do canto 820 L × 870 A × 600 P

Lote A1 · escala 1:10

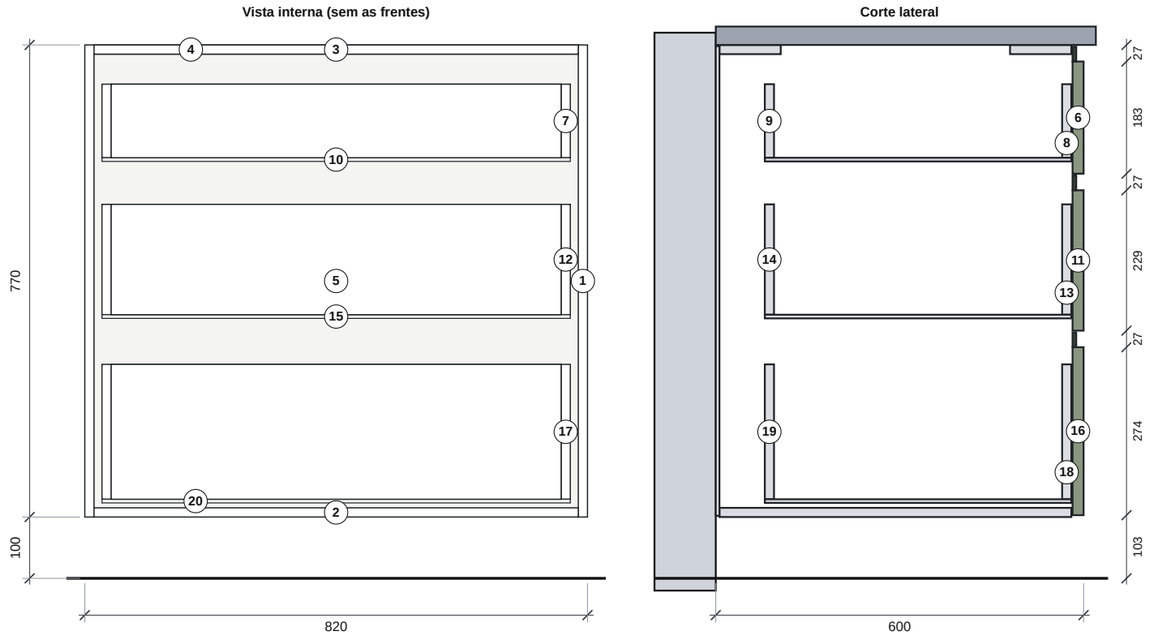

Externo. 3 gavetas verde sálvia com puxador cava no topo de cada frente; a de baixo é a mais alta (proporção do 3D). **Interno.** Gaveta 1 (talheres, caixa de 120 mm) e 2 gavetões (caixas de 180 e 220 mm), corrediças telescópicas de 500 mm. **Abertura.** Gavetas com corrediça telescópica de extração total e amortecimento; puxador cava.


Nº	Peça	Qtd	Comp. × Larg. × Esp.	Material (MDF)	Fita
1	Lateral	2	770 × 574 × 15	Branco TX 15	1C
2	Base	1	790 × 574 × 15	Branco TX 15	1C
3	Travessa superior (frente)	1	790 × 100 × 15	Branco TX 15	1C
4	Travessa superior (fundo)	1	790 × 100 × 15	Branco TX 15	1C
5	Fundo	1	816 × 766 × 6	Branco TX 6	—
6	Frente da gaveta 1	1	817 × 183 × 18	Verde sálvia 18	2C + 2L
7	Gaveta 1: lateral	2	500 × 120 × 15	Branco TX 15	1C
8	Gaveta 1: contrafrente	1	734 × 120 × 15	Branco TX 15	1C
9	Gaveta 1: traseira	1	734 × 120 × 15	Branco TX 15	1C
10	Gaveta 1: fundo	1	764 × 500 × 6	Branco TX 6	—
11	Frente da gaveta 2	1	817 × 229 × 18	Verde sálvia 18	2C + 2L
12	Gaveta 2: lateral	2	500 × 180 × 15	Branco TX 15	1C
13	Gaveta 2: contrafrente	1	734 × 180 × 15	Branco TX 15	1C
14	Gaveta 2: traseira	1	734 × 180 × 15	Branco TX 15	1C
15	Gaveta 2: fundo	1	764 × 500 × 6	Branco TX 6	—
16	Frente da gaveta 3	1	817 × 274 × 18	Verde sálvia 18	2C + 2L
17	Gaveta 3: lateral	2	500 × 220 × 15	Branco TX 15	1C
18	Gaveta 3: contrafrente	1	734 × 220 × 15	Branco TX 15	1C
19	Gaveta 3: traseira	1	734 × 220 × 15	Branco TX 15	1C
20	Gaveta 3: fundo	1	764 × 500 × 6	Branco TX 6	—

Ferragens. 3 par · Corrediça telescópica 500 mm, extração total, com amortecimento *(gavetões: carga ≥ 45 kg)*; 2,451 m · Perfil puxador cava em alumínio, acabamento escuro fosco; 4 un · Pé regulável para rodapé de 100 mm, com clipe; 1 un · Organizador de talheres para gaveta *(opcional — cotar à parte)*

- Encosta no shaft (medida estimada) — o comprimento exato do módulo se ajusta na medição.
- As frentes correm rente à porta do módulo do tanque (T1): ver detalhe do canto na prancha C-05.

M2 Módulo do forno e cooktop 600 L × 870 A × 600 P

Lote A1 · escala 1:10

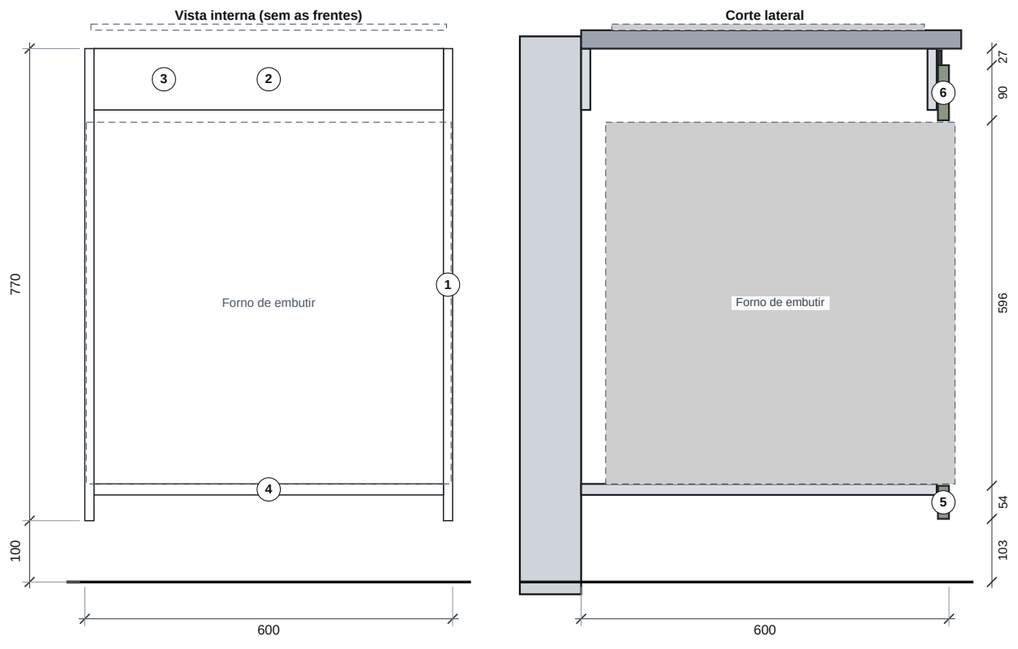

Externo. Forno de embutir à vista; régua fixa de 54 mm embaixo e frente fixa de 114 mm em cima (com a linha do cava alinhada aos vizinhos). **Interno.** Nicho do forno: 570 L × 590 A × 580 P, sem fundo (ventilação e tomada). Sob o tampo, só travessas em pé: o corpo do cooktop ocupa esse espaço. **Abertura.** Sem portas (frentes fixas).

Nº	Peça	Qtd	Comp. × Larg. × Esp.	Material (MDF)	Fita
1	Lateral	2	770 × 580 × 15	Branco TX 15	1C
2	Travessa superior em pé (frente)	1	570 × 100 × 15	Branco TX 15	1C
3	Travessa superior em pé (fundo)	1	570 × 100 × 15	Branco TX 15	1C
4	Base de apoio do forno *(18 mm; recebe o peso do forno)*	1	580 × 570 × 18	Branco TX 18	1L
5	Régua inferior fixa	1	597 × 54 × 18	Verde sálvia 18	2C + 2L
6	Frente fixa superior (sob o cooktop)	1	597 × 90 × 18	Verde sálvia 18	2C + 2L


Ferragens. 0,597 m · Perfil puxador cava em alumínio, acabamento escuro fosco *(decorativo, alinhado aos vizinhos)*; 4 un · Pé regulável para rodapé de 100 mm, com clipe

- Medidas do nicho pelo padrão de forno de embutir de 60 cm — forno e cooktop ainda não definidos: conferir os dois manuais antes de cortar.
- Tomada do forno fora da área do nicho (módulo vizinho ou abaixo), conforme o manual.


M3 Módulo da lava-louças compacta 610 L × 870 A × 600 P

Lote A1 · escala 1:10

Vista interna (sem as frentes)

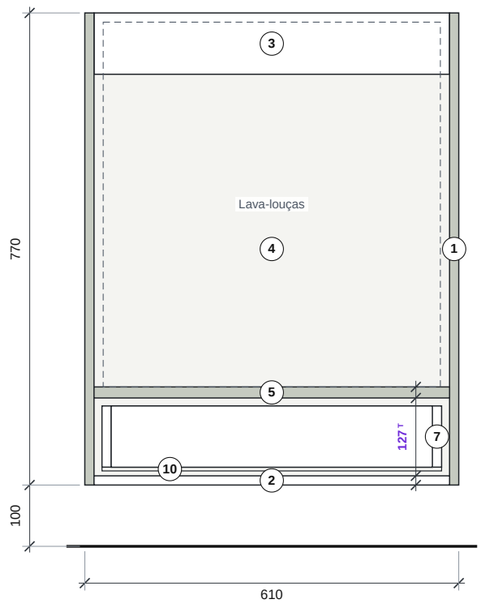

Corte lateral

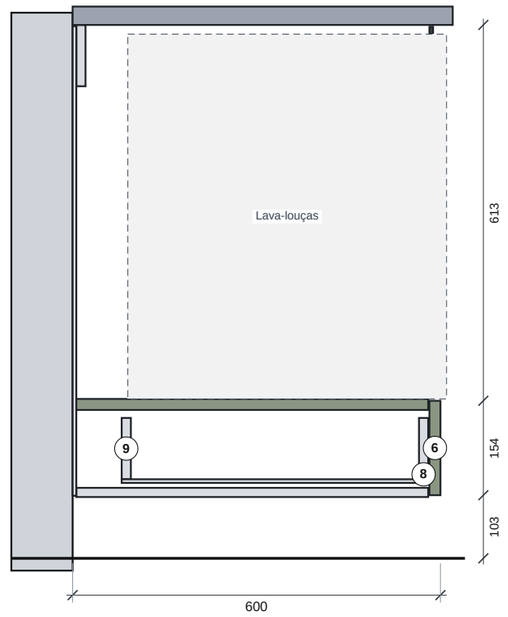

Externo. Lava-louças à vista em nicho elevado; gaveta baixa embaixo (frente lisa de 154 mm, como no 3D). **Interno.** Nicho: 580 L × 595 A × 574 P, laterais internas verdes (ficam à vista ao redor do aparelho). Gaveta inferior com caixa de 100 mm. **Abertura.** Gaveta com corrediça telescópica e abertura por toque (sem puxador, como no 3D).

Nº	Peça	Qtd	Comp. × Larg. × Esp.	Material (MDF)	Fita
1	Lateral	2	770 × 574 × 15	Verde sálvia 15	1C
2	Base	1	580 × 574 × 15	Branco TX 15	1C
3	Travessa superior em pé (fundo)	1	580 × 100 × 15	Branco TX 15	1C
4	Fundo *(recortes para mangueiras e tomada)*	1	766 × 606 × 6	Branco TX 6	—
5	Prateleira de apoio da lava-louças *(18 mm, fixa; aparelho ≈ 30 kg)*	1	580 × 574 × 18	Verde sálvia 18	1C
6	Frente da gaveta inferior *(lisa, abertura por toque)*	1	607 × 154 × 18	Verde sálvia 18	2C + 2L
7	Gaveta inferior: lateral	2	500 × 100 × 15	Branco TX 15	1C
8	Gaveta inferior: contrafrente	1	524 × 100 × 15	Branco TX 15	1C
9	Gaveta inferior: traseira	1	524 × 100 × 15	Branco TX 15	1C
10	Gaveta inferior: fundo	1	554 × 500 × 6	Branco TX 6	—


Ferragens. 1 par · Corrediça telescópica 500 mm com abertura por toque; 4 un · Pé regulável para rodapé de 100 mm, com clipe

- Altura livre do nicho = 595 mm, igual à altura típica do aparelho (folga zero): conferir o modelo; se preciso, reduzir a gaveta de baixo.
- Água, esgoto e tomada pelo módulo da pia (M4): prever furos de passagem na lateral.
- Alternativa para a gaveta: puxador cava como nas demais frentes (muda levemente o visual — depende de autorização).


M4 Armário da pia 700 L × 870 A × 600 P

Lote A1 · escala 1:10

Vista interna (sem as frentes)

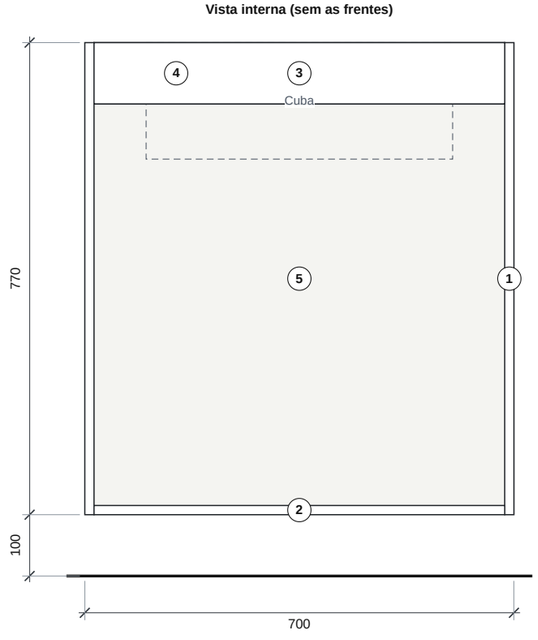

Corte lateral

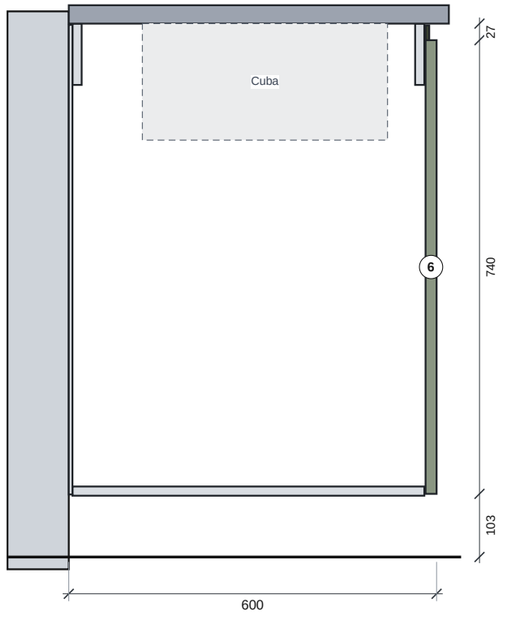

Externo. 2 portas verde sálvia com puxador cava. **Interno.** Vão livre para sifão, registro e lixeira; sem prateleira. Travessas superiores em pé (a cuba ocupa o espaço sob o tampo). Base com proteção contra umidade. **Abertura.** Portas de giro abrindo do centro; dobradiças retas com amortecimento.


Nº	Peça	Qtd	Comp. × Larg. × Esp.	Material (MDF)	Fita
1	Lateral	2	770 × 574 × 15	Branco TX 15	1C
2	Base	1	670 × 574 × 15	Branco TX 15	1C
3	Travessa superior em pé (frente)	1	670 × 100 × 15	Branco TX 15	1C
4	Travessa superior em pé (fundo)	1	670 × 100 × 15	Branco TX 15	1C
5	Fundo *(recortes para água e esgoto)*	1	766 × 696 × 6	Branco TX 6	—
6	Porta	2	740 × 347 × 18	Verde sálvia 18	2C + 2L

Ferragens. 4 un · Dobradiça de caneco 35 mm, reta, com amortecimento; 0,694 m · Perfil puxador cava em alumínio, acabamento escuro fosco; 4 un · Pé regulável para rodapé de 100 mm, com clipe; 1 un · Proteção da base contra umidade (manta de alumínio ou bandeja)

- Posição dos pontos de água e esgoto não consta na planta: levantar no local antes de recortar o fundo.

M5 Armário de 1 porta 360 L × 870 A × 600 P

Lote A1 · escala 1:10

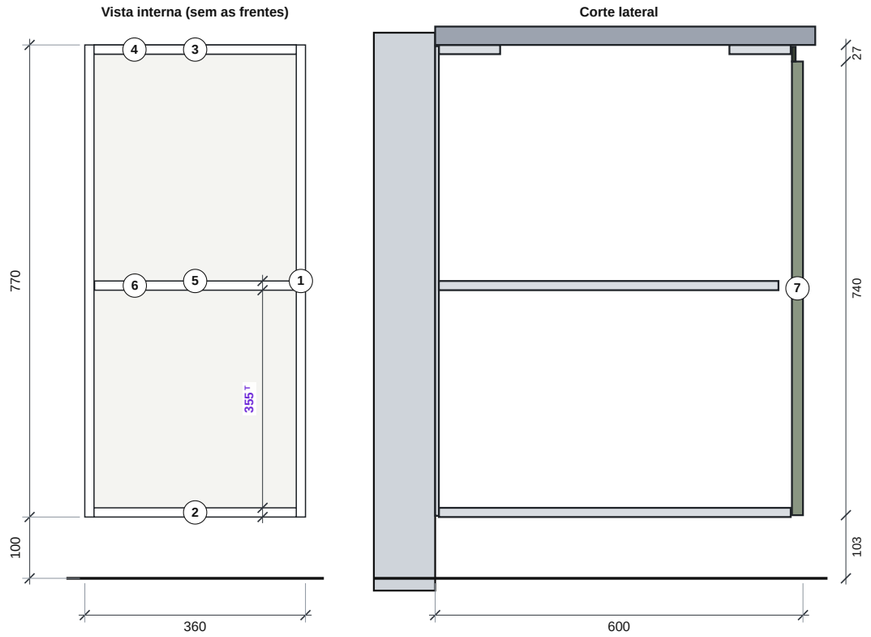


Externo. 1 porta verde sálvia com puxador cava. **Interno.** 1 prateleira regulável (furação para 3 posições). **Abertura.** Porta de giro com dobradiças do lado do painel da geladeira; amortecimento.

Nº	Peça	Qtd	Comp. × Larg. × Esp.	Material (MDF)	Fita
1	Lateral	2	770 × 574 × 15	Branco TX 15	1C
2	Base	1	574 × 330 × 15	Branco TX 15	1L
3	Travessa superior (frente)	1	330 × 100 × 15	Branco TX 15	1C
4	Travessa superior (fundo)	1	330 × 100 × 15	Branco TX 15	1C
5	Fundo	1	766 × 356 × 6	Branco TX 6	—
6	Prateleira regulável	1	554 × 328 × 15	Branco TX 15	1L
7	Porta	1	740 × 357 × 18	Verde sálvia 18	2C + 2L

Ferragens. 2 un · Dobradiça de caneco 35 mm, reta, com amortecimento; 0,357 m · Perfil puxador cava em alumínio, acabamento escuro fosco; 4 un · Pé regulável para rodapé de 100 mm, com clipe; 4 un · Suporte de prateleira (pino metálico 5 mm)

T1 Módulo do tanque (canto cego) 660 L × 870 A × 630 P

Lote A4 · escala 1:10

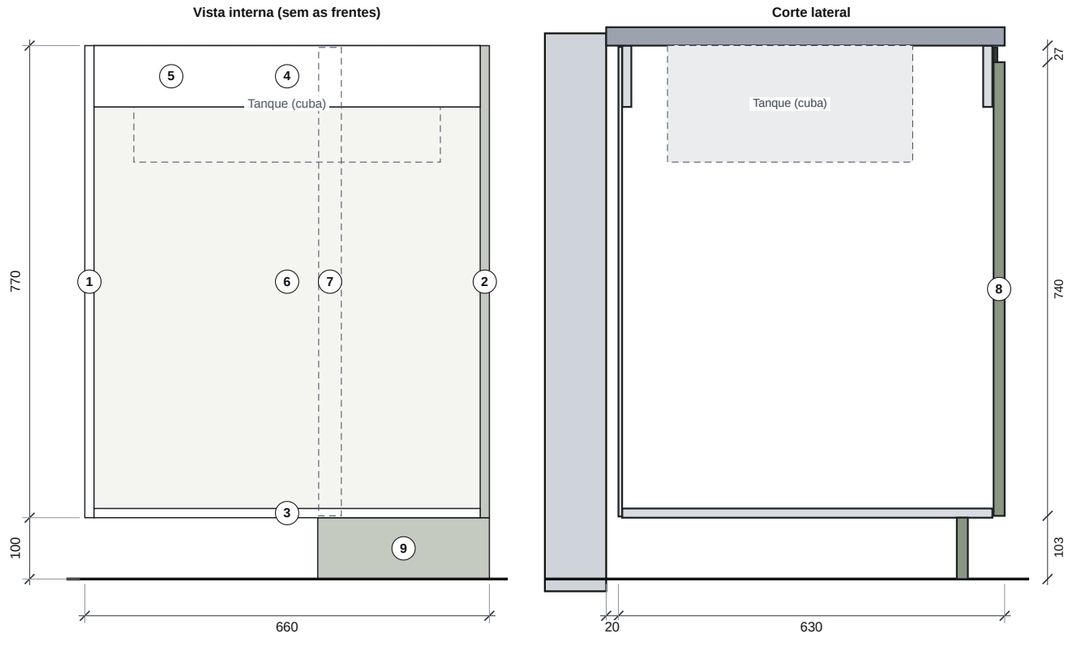

Externo. Do módulo de 660 mm só 280 mm ficam à vista (o resto fica atrás do gaveteiro M1): régua de canto de 40 mm + 1 porta de 237 mm com puxador cava. **Interno.** Vão único sob o tanque (sifão e registros). A parte atrás do M1 é canto cego, acessível pela porta. **Abertura.** Porta de giro com dobradiças do lado da lava e seca (abre para longe das gavetas do M1).

Nº	Peça	Qtd	Comp. × Larg. × Esp.	Material (MDF)	Fita
1	Lateral	1	770 × 604 × 15	Branco TX 15	1C
2	Lateral	1	770 × 604 × 15	Verde sálvia 15	1C
3	Base	1	630 × 604 × 15	Branco TX 15	1C
4	Travessa superior em pé (frente)	1	630 × 100 × 15	Branco TX 15	1C
5	Travessa superior em pé (fundo)	1	630 × 100 × 15	Branco TX 15	1C
6	Fundo *(recortes para água e esgoto do tanque)*	1	766 × 656 × 6	Branco TX 6	—
7	Régua de canto fixa	1	764 × 37 × 18	Verde sálvia 18	2C + 2L
8	Porta	1	740 × 237 × 18	Verde sálvia 18	2C + 2L
9	Rodapé (saia)	1	280 × 100 × 18	Verde sálvia 18	1C

Ferragens. 2 un · Dobradiça de caneco 35 mm, reta, com amortecimento; 0,237 m · Perfil puxador cava em alumínio, acabamento escuro fosco; 4 un · Pé regulável para rodapé de 100 mm, com clipe; 1 un · Proteção da base contra umidade (manta de alumínio ou bandeja)


- Proposta técnica para o canto do L: a régua fixa de 40 mm evita que a porta raspe nas frentes do M1. O 3D mostra o módulo com 2 portas, mas a maior parte fica encoberta.
- Largura depende do shaft (220 mm, estimado) e da lava e seca: conferir no local.
- Lateral voltada para a lava e seca em verde (fica à vista no vão da máquina).

AG Armário sobre a geladeira


750 L × 620 A × 720 P · base a 1980 do piso

Lote A2 · escala 1:10

Vista interna (sem as frentes)

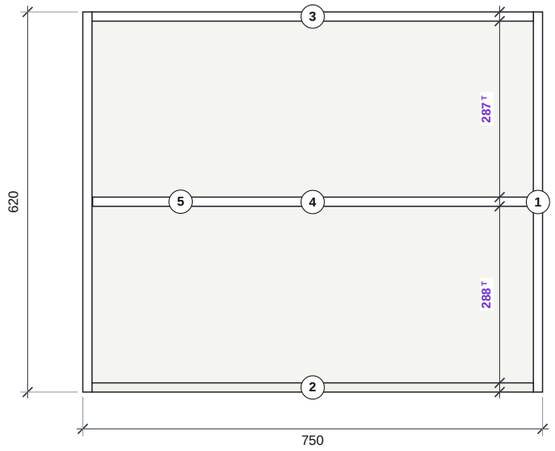

Corte lateral

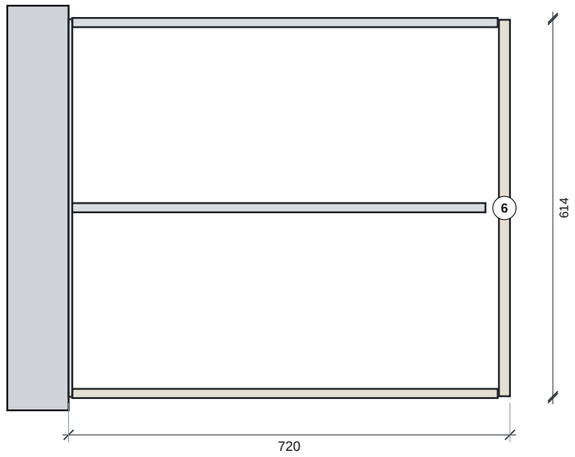

Externo. 2 portas off-white lisas, sem puxador, até o teto. **Interno.** 1 prateleira regulável. Base aparente (vista por baixo, acima da geladeira) em off-white. **Abertura.** Portas de giro abrindo do centro, com fecho toque (dobradiças sem amortecedor).

Nº	Peça	Qtd	Comp. × Larg. × Esp.	Material (MDF)	Fita
1	Lateral	2	694 × 620 × 15	Branco TX 15	1L
2	Base	1	720 × 694 × 15	Off-white 15	1C
3	Tampo	1	720 × 694 × 15	Branco TX 15	1C
4	Fundo	1	746 × 616 × 6	Branco TX 6	—
5	Prateleira regulável	1	718 × 674 × 15	Branco TX 15	1C
6	Porta	2	614 × 372 × 18	Off-white 18	2C + 2L

Ferragens. 4 un · Dobradiça de caneco 35 mm, reta, sem amortecedor; 2 un · Fecho toque (pulsador); 4 un · Suporte de prateleira (pino metálico 5 mm); 2 par · Suporte de fixação de armário aéreo, regulável


- Altura = pé-direito − 1980 mm. Com pé-direito de 2600 mm (estimado) dá 620 mm; prever régua de ajuste no teto.
- Encosta na parede do fundo: prever régua de ajuste de prumo.

NM Nicho do micro-ondas


630 L × 350 A × 400 P · base a 1550 do piso

Lote A3 · escala 1:10

Vista interna (sem as frentes)

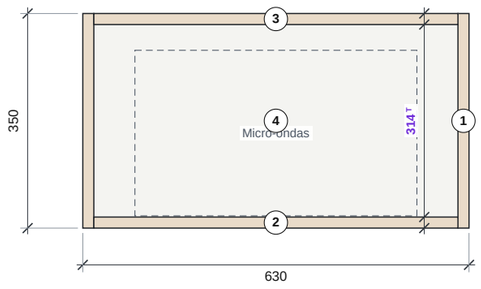

Corte lateral

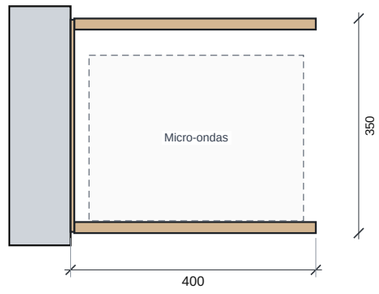

Externo. Nicho aberto em madeira clara, 18 mm, 40 mm mais fundo que a faixa verde e 80 mm mais fundo que o aéreo de madeira. **Interno.** Vão livre: 594 L × 314 A × 394 P. Fundo no padrão madeira, com furo para a tomada. **Abertura.** Aberto.

Nº	Peça	Qtd	Comp. × Larg. × Esp.	Material (MDF)	Fita
1	Lateral	2	394 × 350 × 18	Madeira clara 18	1L
2	Base	1	594 × 394 × 18	Madeira clara 18	1C
3	Tampo	1	594 × 394 × 18	Madeira clara 18	1C
4	Fundo	1	626 × 346 × 6	Madeira clara 6	—

Ferragens. 2 par · Suporte de fixação de armário aéreo, regulável


- Micro-ondas típico de 460 × 270 × 350 mm (modelo não informado): conferir a ventilação pedida no manual.

AS Aéreo superior off-white


3090 L × 620 A × 360 P · base a 1980 do piso

Lote A3 · escala 1:12,5

Vista interna (sem as frentes)

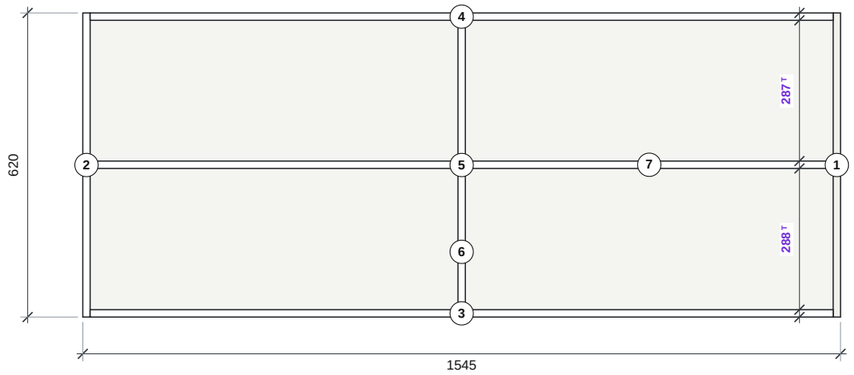

Corte lateral

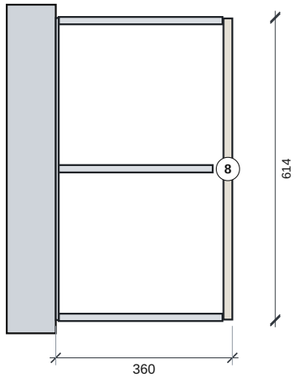

Externo. 4 portas off-white lisas de 769,5 × 614 mm, sem puxador, até o teto. **Interno.** 2 caixas de 2 portas; divisória central e 1 prateleira regulável por vão (4 vãos). **Abertura.** Portas de giro em pares, abrindo do centro de cada caixa, com fecho toque (dobradiças sem amortecedor).

Nº	Peça	Qtd	Comp. × Larg. × Esp.	Material (MDF)	Fita
1	Lateral	1	620 × 334 × 15	Off-white 15	1C
2	Lateral	3	620 × 334 × 15	Branco TX 15	1C
3	Base	2	1515 × 334 × 15	Branco TX 15	1C
4	Tampo	2	1515 × 334 × 15	Branco TX 15	1C
5	Fundo	2	1541 × 616 × 6	Branco TX 6	—
6	Divisória central	2	590 × 334 × 15	Branco TX 15	1C
7	Prateleira regulável	4	748 × 314 × 15	Branco TX 15	1C
8	Porta	4	769,5 × 614 × 18	Off-white 18	2C + 2L

Ferragens. 12 un · Dobradiça de caneco 35 mm, reta, sem amortecedor *(3 por porta (largura acima de 600 mm))*; 4 un · Fecho toque (pulsador); 16 un · Suporte de prateleira (pino metálico 5 mm); 4 par · Suporte de fixação de armário aéreo, regulável


- Desenhada a 1ª das 2 caixas (a 2ª é igual, com as duas laterais brancas). A lista traz as duas.
- Altura = pé-direito − 1980 mm. Com pé-direito de 2600 mm (estimado) dá 620 mm; prever régua de ajuste no teto.
- Portas de 769,5 mm de largura: acima do usual para porta de giro (até ≈ 600 mm). Mantido o desenho aprovado (4 portas), com 3 dobradiças por porta. Alternativa: 6 portas de ≈ 512 mm — só com autorização.
- Lateral da ponta do shaft fica à vista: em off-white.

AM Aéreo inferior em madeira clara


2460 L × 350 A × 320 P · base a 1550 do piso

Lote A3 · escala 1:20

Vista interna (sem as frentes)

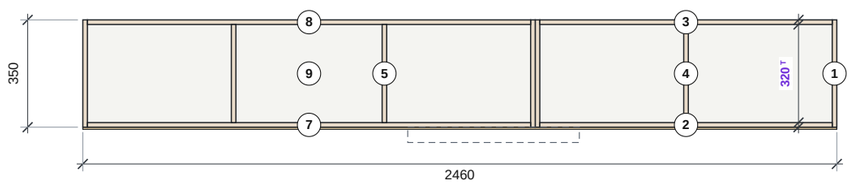

Corte lateral

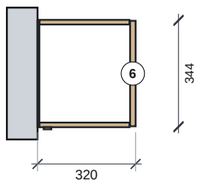

Externo. 5 portas em madeira clara de 489 × 344 mm, sem puxador. Recuado 40 mm em relação à faixa verde. **Interno.** 2 caixas (2 + 3 portas), um vão por porta, sem prateleira. Base e lateral da ponta do shaft ficam à vista: caixa no padrão madeira. **Abertura.** Portas de giro com fecho toque (dobradiças sem amortecedor).

Nº	Peça	Qtd	Comp. × Larg. × Esp.	Material (MDF)	Fita
1	Lateral	4	350 × 294 × 15	Madeira clara 15	1C
2	Base	1	954 × 294 × 15	Madeira clara 15	1C
3	Tampo	1	954 × 294 × 15	Madeira clara 15	1C
4	Fundo	1	980 × 346 × 6	Branco TX 6	—
5	Divisória	3	320 × 294 × 15	Madeira clara 15	1C
6	Porta	5	489 × 344 × 18	Madeira clara 18	2C + 2L
7	Base	1	1446 × 294 × 15	Madeira clara 15	1C
8	Tampo	1	1446 × 294 × 15	Madeira clara 15	1C
9	Fundo	1	1472 × 346 × 6	Branco TX 6	—

Ferragens. 10 un · Dobradiça de caneco 35 mm, reta, sem amortecedor *(2 delas curvas (meia sobreposição): a porta do meio da caixa de 3 fica presa na divisória)*; 5 un · Fecho toque (pulsador); 4 par · Suporte de fixação de armário aéreo, regulável; 2,46 m · Perfil de alumínio de embutir com difusor + fita de LED 2700–3000 K *(opcional — cotar à parte)*; 1 un · Fonte (driver) para a fita de LED *(opcional — cotar à parte)*

- O depurador fica sob este aéreo, acima do cooktop: o modelo ainda não foi definido — conferir se exige recorte na base/fundo e tomada dentro do aéreo.
- Fita de LED em perfil embutido na base, junto ao frontão (tom quente).

DOCUMENTO	PRANCHA	ESCALA	UNIDADE	REVISÃO · DATA	FOLHA
Caderno de marcenaria Projeto executivo para orçamento	**C-11 — Cozinha · módulos AS e AM**	**1:12,5 e 1:20**	**mm**	**00 · 13/11/2026**	**13/28**

PG Painel lateral da torre da geladeira 30 × 2600 × 750 (L × A × P)

Lote A2

Descrição. Painel off-white de 30 mm (engrossado), do piso ao teto, 750 mm de profundidade.

Nº	Peça	Qtd	Comp. × Larg. × Esp.	Material (MDF)	Fita
1	Painel lateral (engrossado 30 mm) *(2 chapas de 15 mm coladas; 2 faces aparentes)*	2	2600 × 750 × 15	Off-white 15	1C

Ferragens. 1 cj · Fixação de painel (cantoneiras, parafusos e cola PU)

- Altura = pé-direito (2600 mm, estimado): cortar na medida real, com folga de montagem.
- A bancada, o frontão e os aéreos morrem neste painel.

FV Faixa verde entre os aéreos 3090 × 80 × 360 (L × A × P)

Lote A3

Descrição. Faixa verde sálvia de 80 mm de altura em toda a extensão dos aéreos, no mesmo plano do aéreo superior. Vazio de 80 mm atrás da régua: passagem da fiação e alojamento da fonte do LED.

Nº	Peça	Qtd	Comp. × Larg. × Esp.	Material (MDF)	Fita
1	Régua frontal	2	1545 × 80 × 18	Verde sálvia 18	2C + 1L
2	Fechamento inferior	1	1527 × 60 × 18	Verde sálvia 18	1C
3	Fechamento inferior	1	1545 × 60 × 18	Verde sálvia 18	1C
4	Tampa lateral (ponta do shaft)	1	342 × 80 × 18	Verde sálvia 18	2C

Ferragens. —

- Em 2 peças, com emenda alinhada ao encontro das portas do aéreo superior (a chapa tem 2.750 mm).

RA Rodapé da bancada (parede A) 3090 × 100 × 18 (L × A × P)

Lote A1

Descrição. Rodapé recuado 60 mm do plano das frentes, altura 100 mm, do canto ao painel da geladeira.

Nº	Peça	Qtd	Comp. × Larg. × Esp.	Material (MDF)	Fita
1	Rodapé (saia) *(removível, preso por clipes aos pés)*	2	1545 × 100 × 18	Verde sálvia 18	1C

Ferragens. —

- No 3D o rodapé aparece em verde mais fechado que as frentes. Para orçamento: mesmo padrão verde das frentes — confirmar se prefere tom mais escuro.

Imagens do modelo 3D aprovado, para comparar com os desenhos técnicos. Cores e proporções são as do projeto; os aparelhos são representações genéricas.



Parede A de frente (sem a divisória da sala) — comparar com a elevação C-02



Vista a partir da entrada da cozinha




Área de serviço: tanque, lava e seca e canto do L — comparar com C-05



Torre da geladeira: painel lateral e armário superior

DOCUMENTO	PRANCHA	ESCALA	UNIDADE	REVISÃO · DATA	FOLHA
Caderno de marcenaria Projeto executivo para orçamento	**C-13 — Cozinha · imagens 3D**	**—**	**mm**	**00 · 13/11/2026**	**15/28**

Origem das medidas: **P** cota escrita na planta da construtora · **E** estimada pela escala da planta — conferir no local · **A** aparelho com medida típica — conferir o modelo · **T** proposta técnica do interior — a aprovar · **sem marca** medida do móvel no 3D aprovado

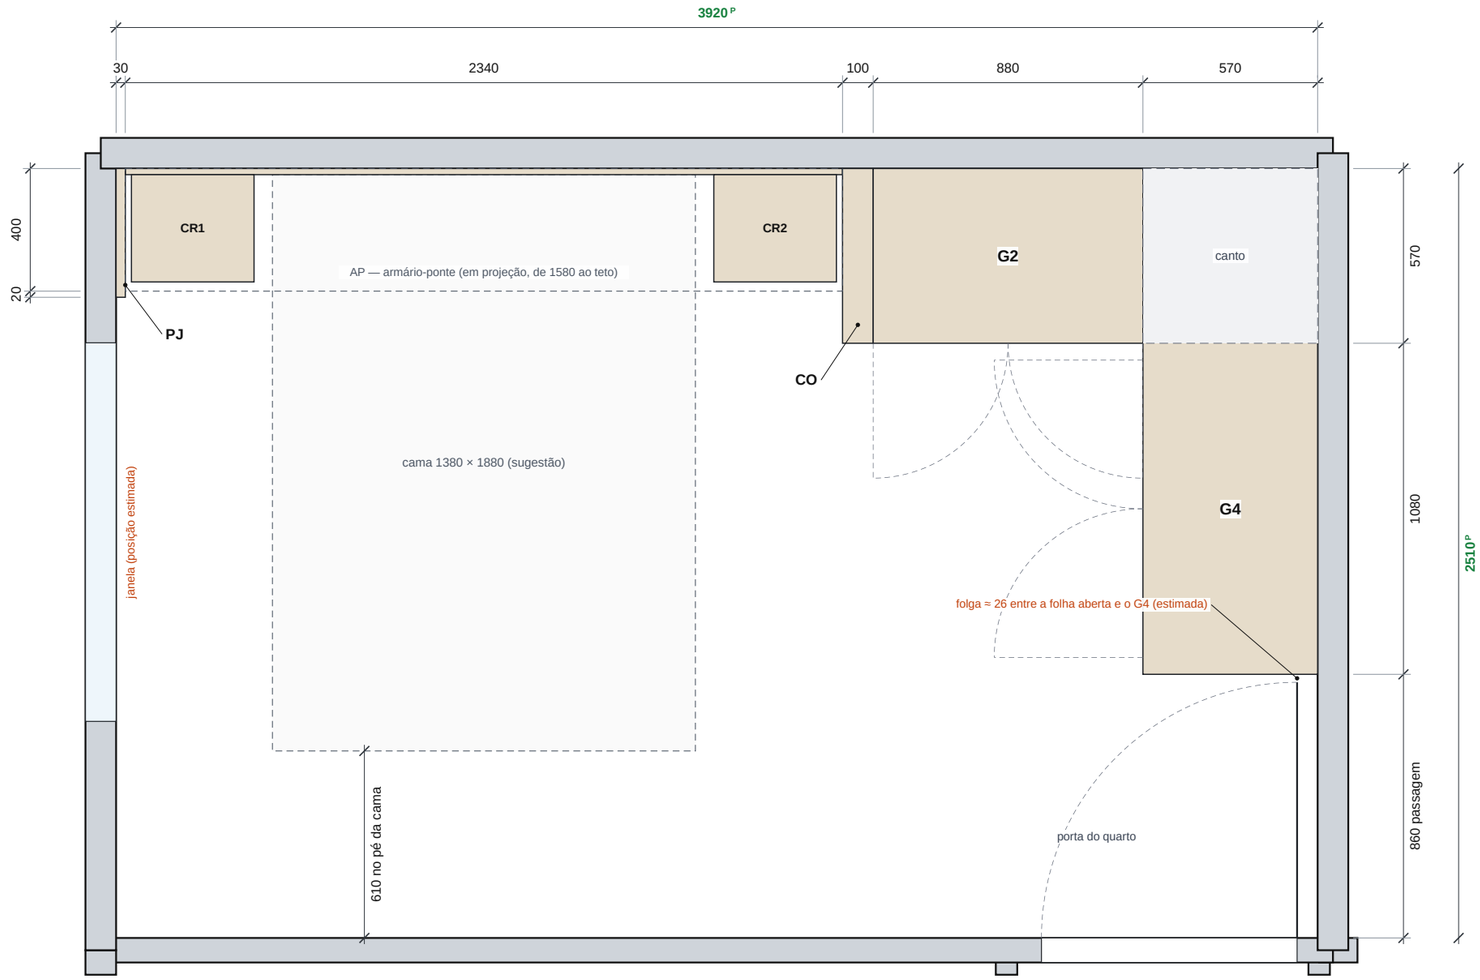


Cód.	Módulo	Lote	L × A × P	Base a	Frentes e acabamento	Peças	MDF m²
CO	Coluna em carvalho	B1	100 × 2600 × 570	piso	Coluna de 100 × 570 mm, do piso ao teto, em carvalho claro: separa o armário-ponte do guarda-roupa.	6	1,73
G2	Guarda-roupa de portas de espelho	B1	880 × 2600 × 570	piso	2 portas de 437 × 2514 mm revestidas de espelho, puxador barra de 300 mm, rodapé cinza recuado de 80 mm.	10	9,04
G4	Guarda-roupa de portas cinza + canto	B2	1650 × 2600 × 570	piso	2 portas cinza de 482 × 2514 mm embutidas entre molduras de carvalho de 55 mm; lateral aparente em carvalho; rodapé cinza recuado. O canto de 570 × 570 mm fica atrás do G2 e é aproveitado por dentro.	49	20,79
AP	Armário-ponte sobre a cama	C1	2340 × 1020 × 400	1580	6 portas em carvalho claro de 387 × 1014 mm, sem puxador, do topo da cabeceira ao teto.	27	10,28
PJ	Painel lateral da ponte (lado da janela)	C2	30 × 2600 × 420	piso	Painel em carvalho de 30 mm (engrossado), 420 mm de profundidade, do piso ao teto.	2	2,18
CB	Cabeceira em painel	C3	2340 × 1580 × 20	piso	3 painéis de carvalho de 18 mm com 2 frisos verticais (juntas de 10 mm com fundo escuro), do piso à base do armário-ponte.	3	3,67
CR1	Criado suspenso 1	C4	400 × 100 × 350	420	Criado suspenso em carvalho de 400 × 100 × 350 mm, a 420 mm do piso, 1 gaveta sem puxador.	11	0,54
CR2	Criado suspenso 2	C4	400 × 100 × 350	420	Criado suspenso em carvalho de 400 × 100 × 350 mm, a 420 mm do piso, 1 gaveta sem puxador.	11	0,54

Origem das medidas: **P** cota escrita na planta da construtora · **E** estimada pela escala da planta — conferir no local · **A** aparelho com medida típica — conferir o modelo · **T** proposta técnica do interior — a aprovar · **sem marca** medida do móvel no 3D aprovado

Elevação A — vista externa

Parede da cabeceira: painel, armário-ponte, cabeceira, criados, coluna e guarda-roupa de espelho. À direita, a lateral do G4.

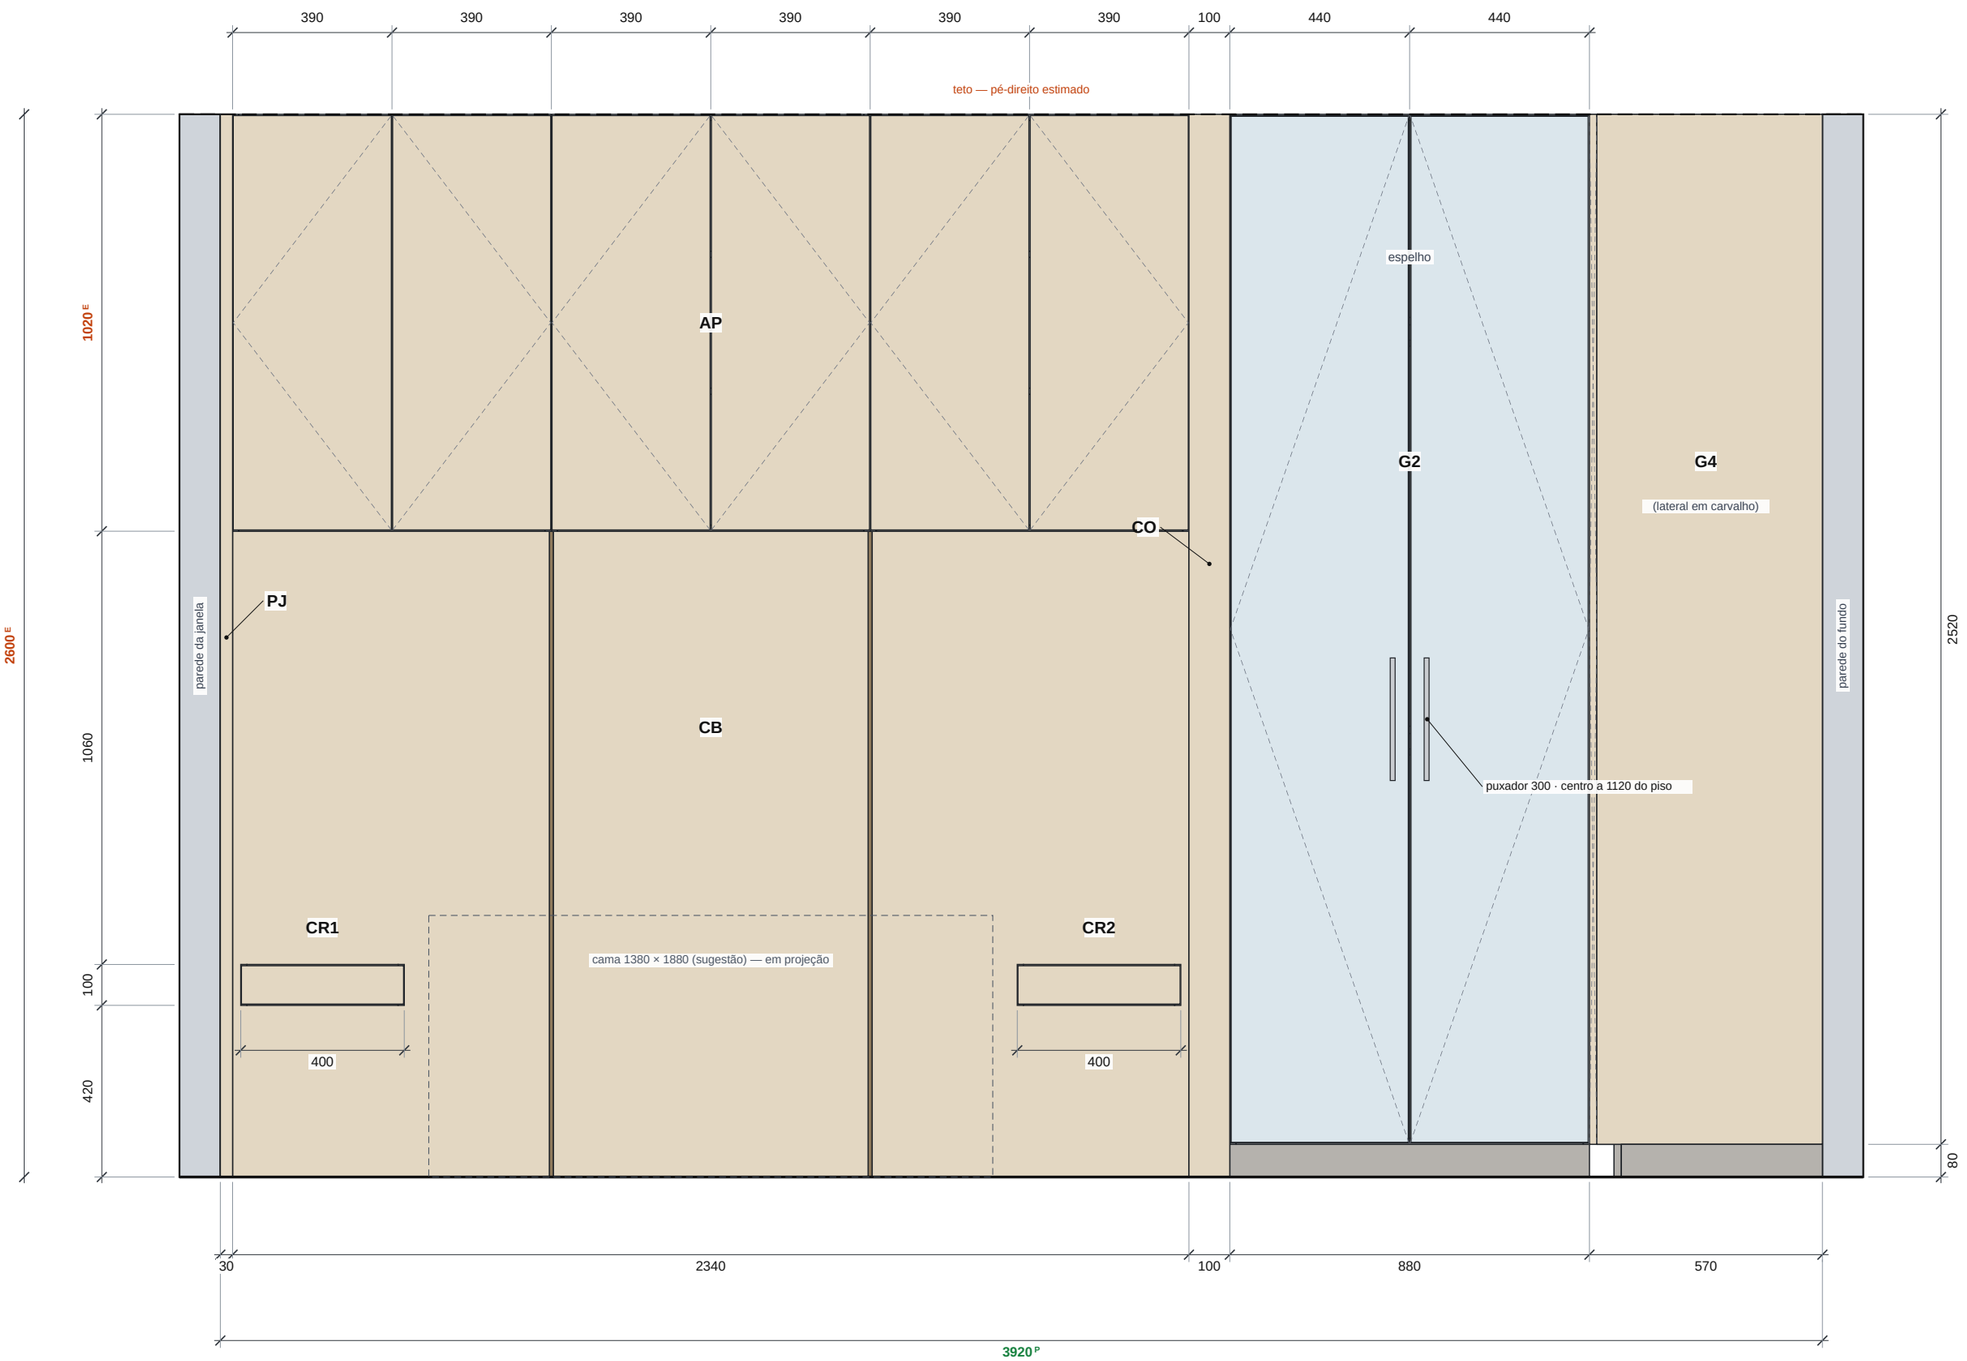


DOCUMENTO	PRANCHA	ESCALA	UNIDADE	REVISÃO · DATA	FOLHA
Caderno de marcenaria Projeto executivo para orçamento	**G-02 — Suíte · elevação A — vista externa**	**1:15**	**mm**	**00 · 13/11/2026**	**17/28**

Origem das medidas: **P** cota escrita na planta da construtora · **E** estimada pela escala da planta — conferir no local · **A** aparelho com medida típica — conferir o modelo · **T** proposta técnica do interior — a aprovar · **sem marca** medida do móvel no 3D aprovado

Elevação A — vista interna (sem as portas)


Interior proposto: cabideiro duplo no G2 e prateleiras no armário-ponte.

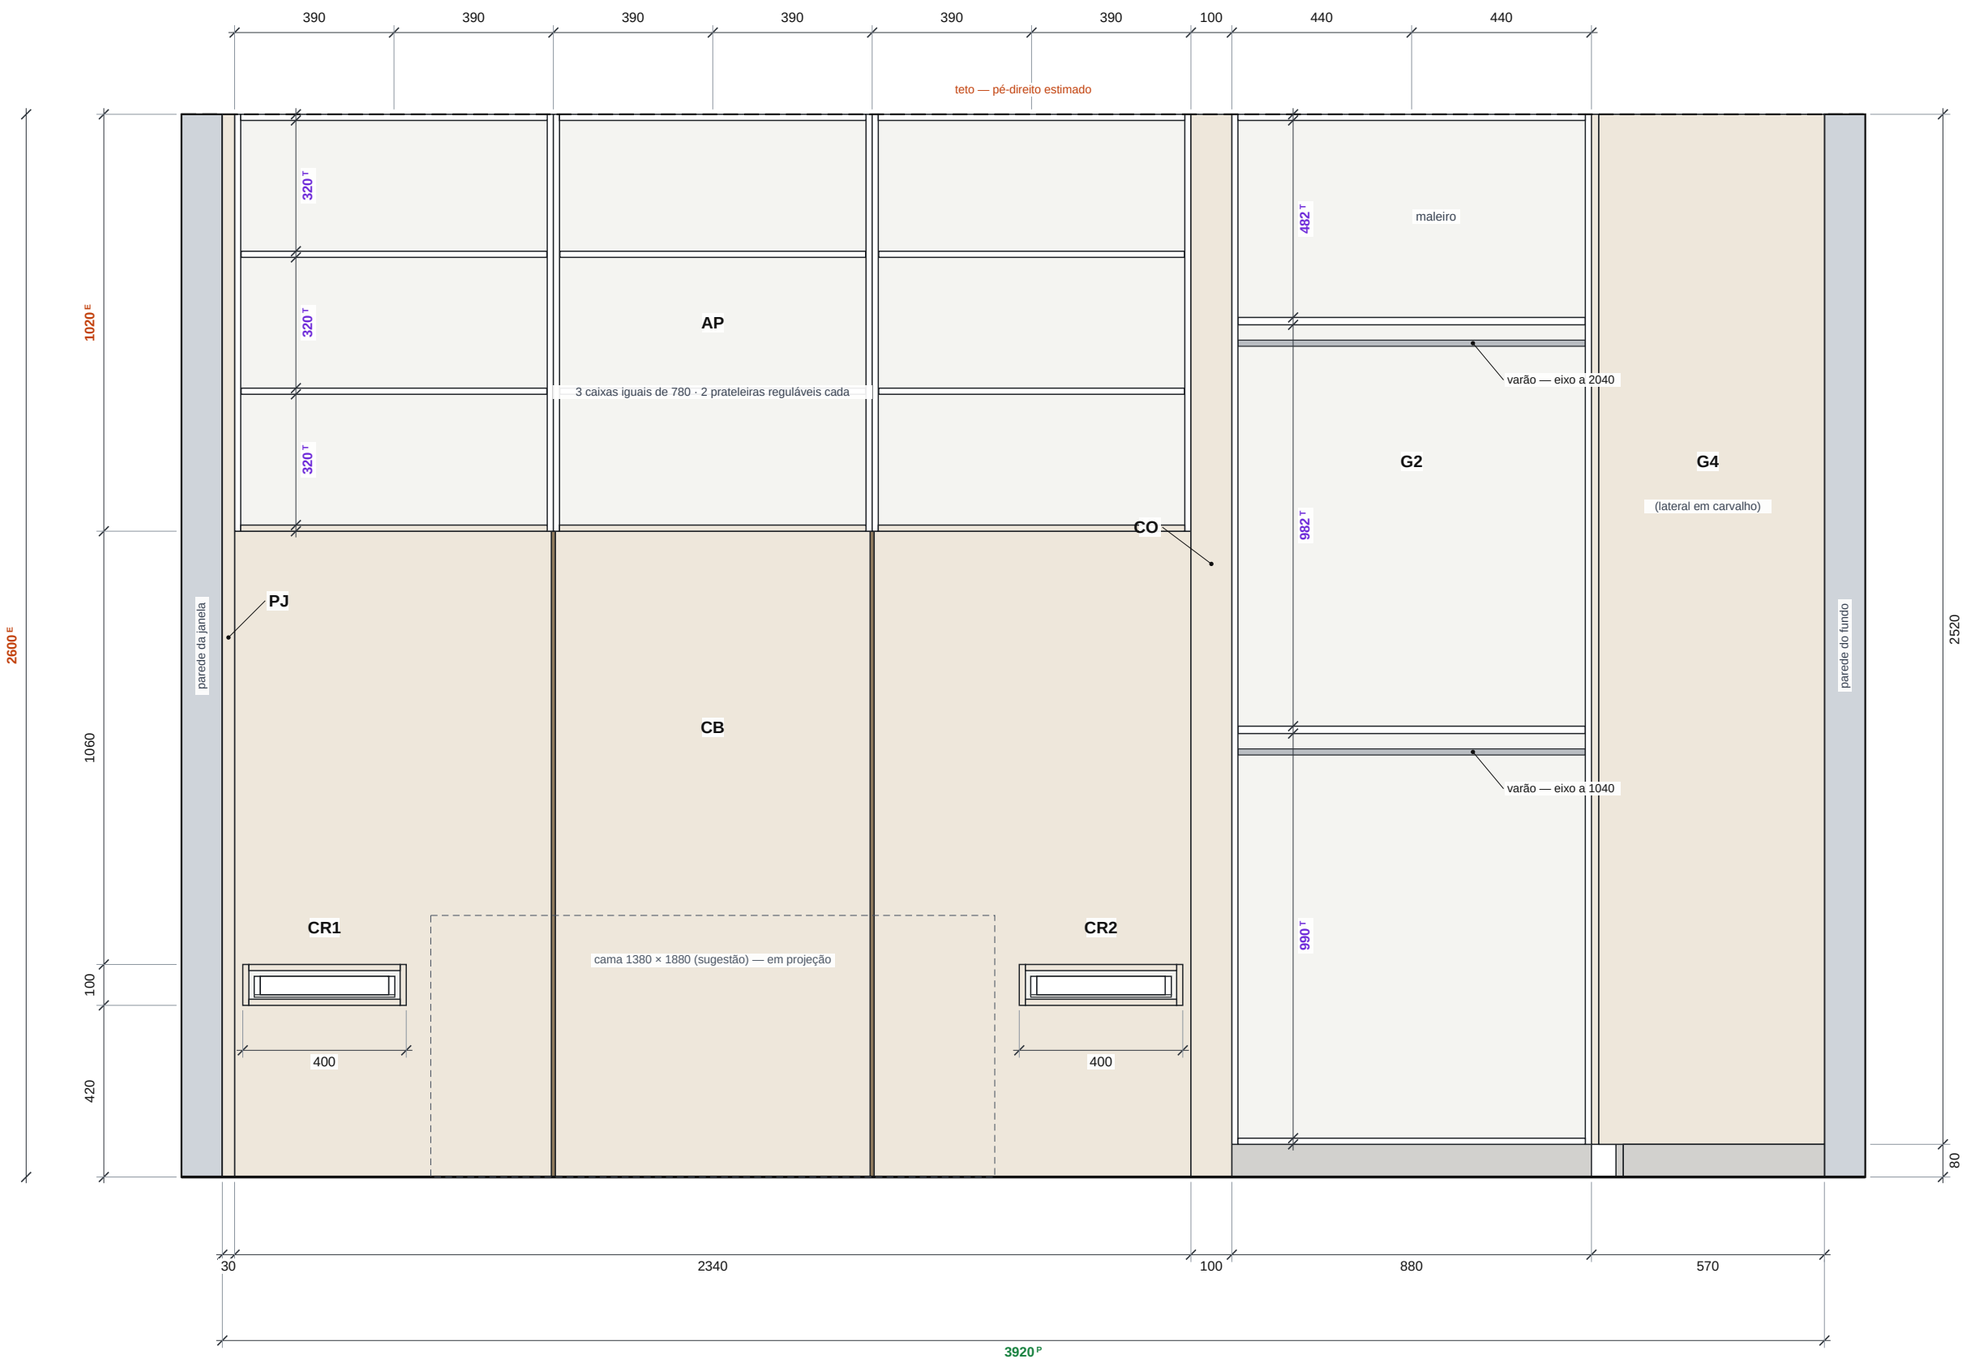


DOCUMENTO **Caderno de marcenaria** Projeto executivo para orçamento	PRANCHA **G-03 — Suíte · elevação A — vista interna**	ESCALA **1:15**	UNIDADE **mm**	REVISÃO · DATA **00 · 13/11/2026**	FOLHA **18/28**

Origem das medidas: **P** cota escrita na planta da construtora · **E** estimada pela escala da planta — conferir no local · **A** aparelho com medida típica — conferir o modelo · **T** proposta técnica do interior — a aprovar · **sem marca** medida do móvel no 3D aprovado

Elevação B — vista externa

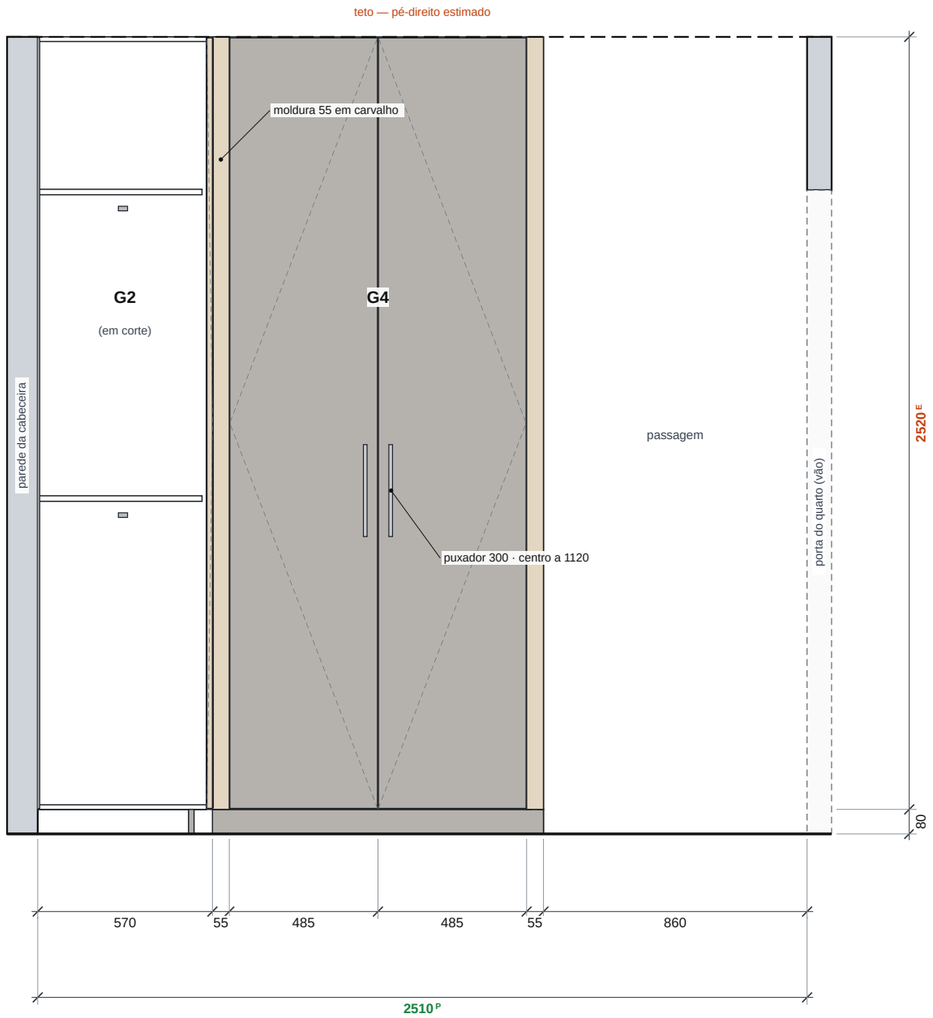

Elevação B — vista interna (G4 + canto, sem as portas)

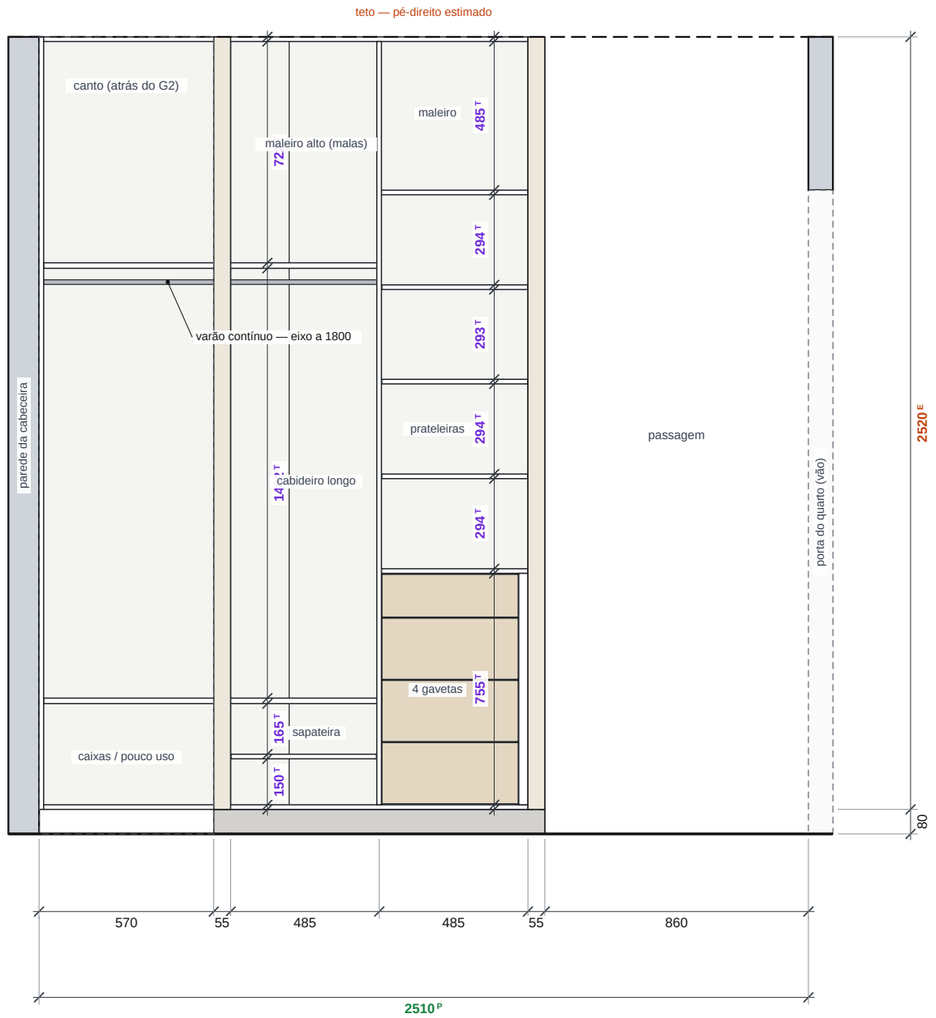

DOCUMENTO	PRANCHA	ESCALA	UNIDADE	REVISÃO · DATA	FOLHA
Caderno de marcenaria Projeto executivo para orçamento	**G-04 — Suíte · elevação B — vistas externa e interna**	**1:20**	**mm**	**00 · 13/11/2026**	**19/28**


Origem das medidas: **P** cota escrita na planta da construtora · **E** estimada pela escala da planta — conferir no local · **A** aparelho com medida típica — conferir o modelo · **T** proposta técnica do interior — a aprovar · **sem marca** medida do móvel no 3D aprovado

Cortes do guarda-roupa e dos complementos

Corte 1: AP · CB · CR1 · Corte 2: G2 — cabideiro duplo · Corte 3: canto (atrás do G2) · Corte 4: G4 — sapateira e cabideiro longo · Corte 5: G4 — gavetas e prateleiras. Cortes 1 e 2 pela parede A; 3 a 5 pela parede B.


Corte 1

AP · CB · CR1

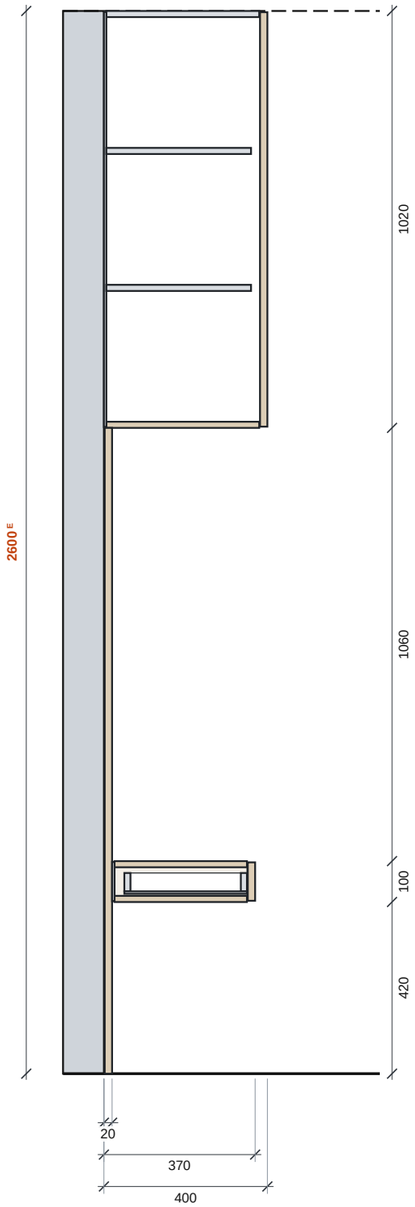


Corte 2

G2 — cabideiro duplo

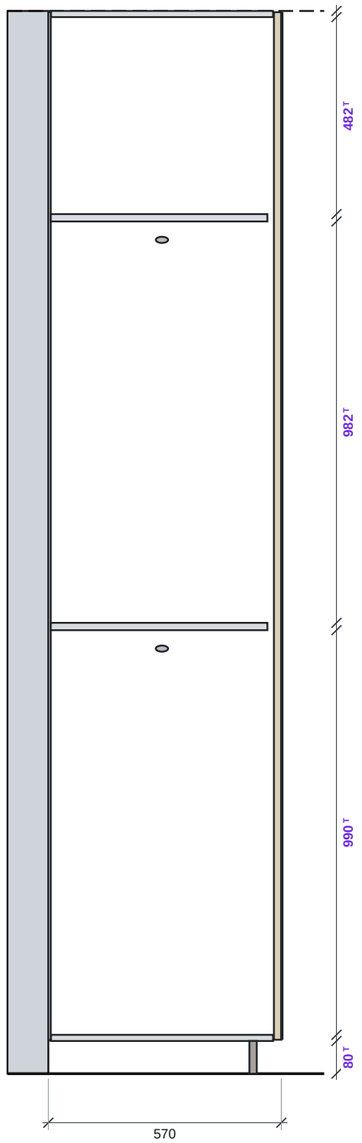


Corte 3

canto (atrás do G2)

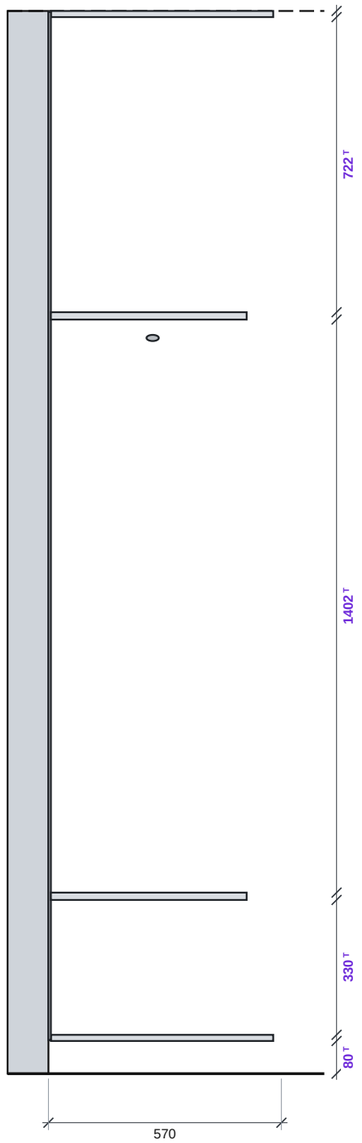


Corte 4

G4 — sapateira e cabideiro longo

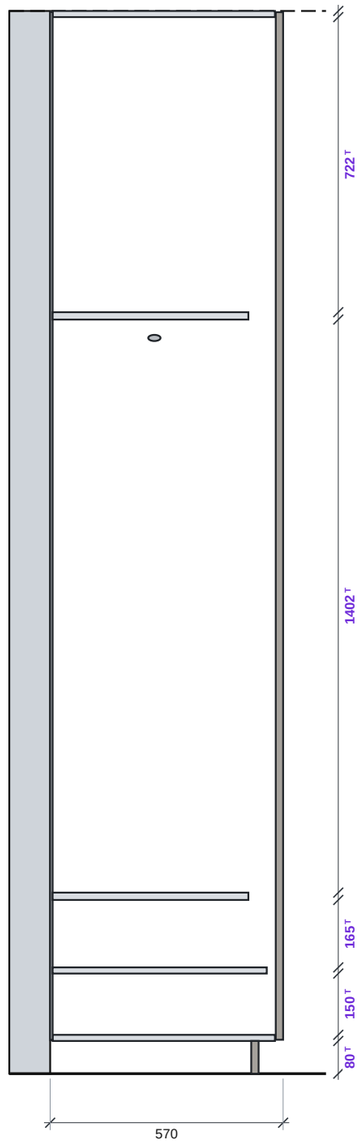

Corte 5


G4 — gavetas e prateleiras

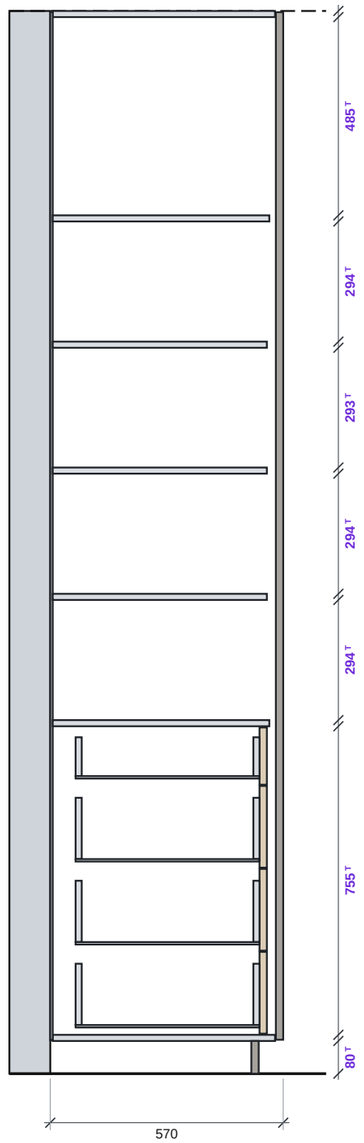

DOCUMENTO	PRANCHA	ESCALA	UNIDADE	REVISÃO · DATA	FOLHA
Caderno de marcenaria Projeto executivo para orçamento	**G-05 — Suíte · cortes**	**1:15**	**mm**	**00 · 13/11/2026**	**20/28**

G2 Guarda-roupa de portas de espelho 880 L × 2600 A × 570 P

Lote B1 · escala 1:20

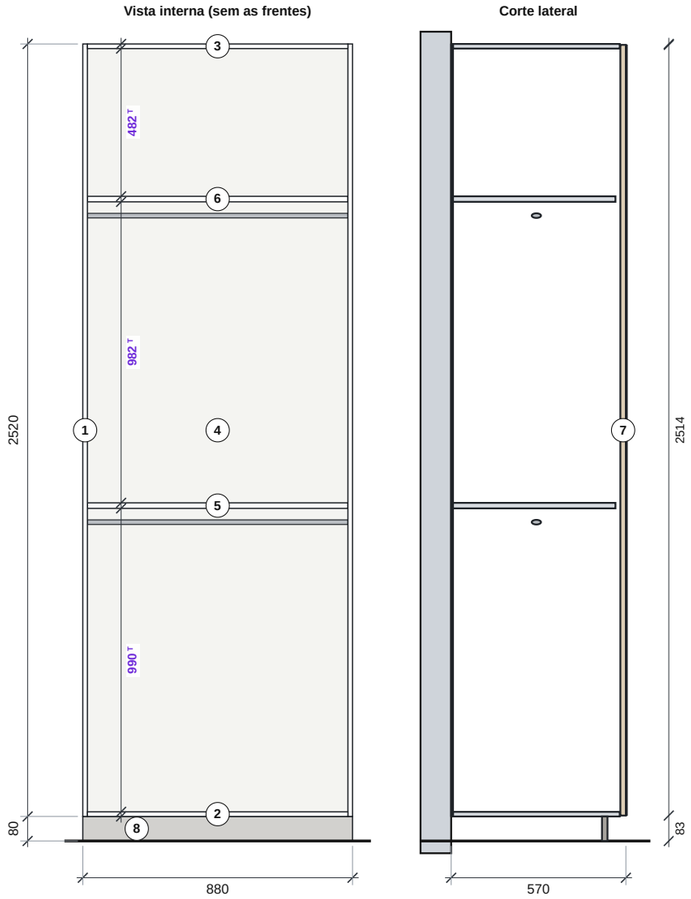

Externo. 2 portas de 437 × 2514 mm revestidas de espelho, puxador barra de 300 mm, rodapé cinza recuado de 80 mm. **Interno.** PROPOSTA — cabideiro duplo em vão único de 850 mm: varão baixo a 1040 mm e varão alto a 2040 mm (camisas, blazers, calças dobradas), maleiro de 482 mm no topo. **Abertura.** Portas de giro abrindo do centro, dobradiças retas com amortecimento (5 por porta) e tensor embutido.

Nº	Peça	Qtd	Comp. × Larg. × Esp.	Material (MDF)	Fita
1	Lateral	2	2520 × 544 × 15	Branco TX 15	1C
2	Base	1	850 × 544 × 15	Branco TX 15	1C
3	Tampo	1	850 × 544 × 15	Branco TX 15	1C
4	Fundo	1	2516 × 876 × 6	Branco TX 6	—
5	Prateleira fixa entre os varões	1	850 × 530 × 18	Branco TX 18	1C
6	Prateleira do maleiro	1	850 × 530 × 18	Branco TX 18	1C
7	Porta (base do espelho)	2	2514 × 437 × 18	Carvalho claro 18	2C + 2L
8	Rodapé frontal	1	880 × 80 × 18	Cinza 18	1C

Ferragens. 10 un · Dobradiça de caneco 35 mm, reta, com amortecimento; 2 un · Tensor (esticador) de porta embutido; 2 un · Puxador barra reta 300 mm, alumínio ou inox escovado *(fixado através do espelho (2 furos por porta))*; 2,174 m² · Espelho prata 3 mm, bordas lapidadas *(2 peças de 433 × 2510 mm, 3 mm, bordas lapidadas)*; 1,7 m · Tubo cabideiro oblongo 30 × 15 mm em alumínio; 4 un · Suporte lateral para tubo cabideiro; 4 un · Pé regulável para rodapé de 80 mm, com clipe

- Portas inteiras de 2514 mm (pé-direito de 2600 mm, estimado): exigem tensor e montagem no local.
- A porta do lado do canto abre contra a frente do G4: limitar a abertura a 90° (dobradiça com limitador). Alternativa: régua de 40 mm em carvalho junto ao canto — muda a paginação; só com autorização.
- Varão alto a 2,04 m: confortável para quem alcança ≈ 2,0 m. Alternativa: cabideiro basculante (cotar à parte).

CO Coluna em carvalho 100 × 2600 × 570 (L × A × P)

Lote B1

Descrição. Coluna de 100 × 570 mm, do piso ao teto, em carvalho claro: separa o armário-ponte do guarda-roupa. Oca (frente + lateral aparente em L, com travas internas). Pode receber a fiação dos interruptores da cabeceira.

Nº	Peça	Qtd	Comp. × Larg. × Esp.	Material (MDF)	Fita
1	Frente da coluna	1	2600 × 100 × 18	Carvalho claro 18	2C
2	Lateral aparente (lado da cama)	1	2600 × 552 × 18	Carvalho claro 18	1C
3	Trava interna	4	100 × 82 × 15	Branco TX 15	—

Ferragens. 1 cj · Fixação de painel (cantoneiras, parafusos e cola PU)


- Altura = pé-direito (2600 mm, estimado).

G4 Guarda-roupa de portas cinza + canto


1650 L × 2600 A × 570 P

Lote B2 · escala 1:15

Vista interna (sem as frentes)

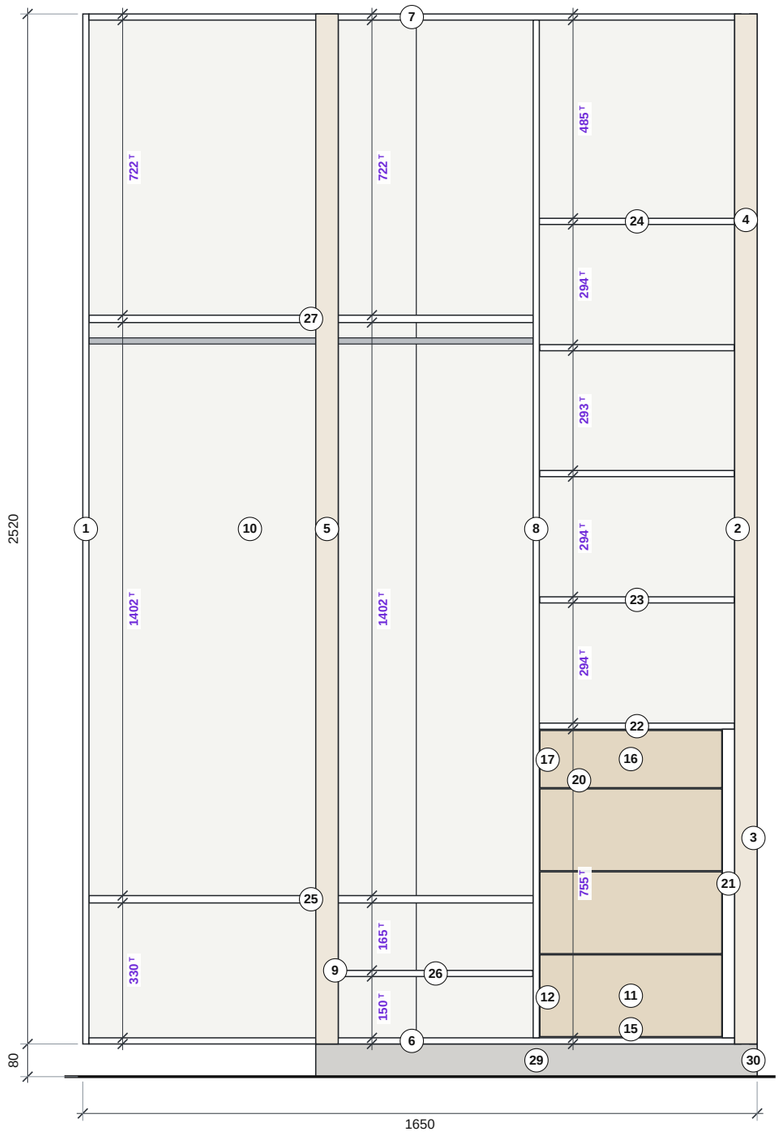

Corte lateral

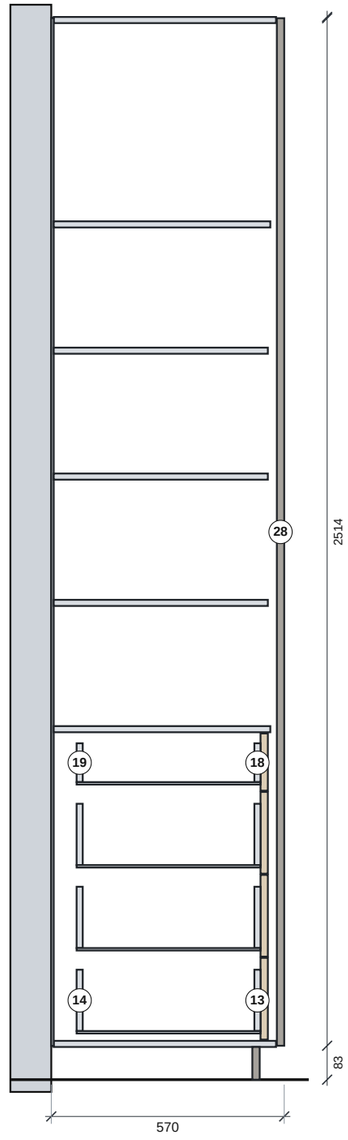

Externo. 2 portas cinza de 482 × 2514 mm embutidas entre molduras de carvalho de 55 mm; lateral aparente em carvalho; rodapé cinza recuado. O canto de 570 × 570 mm fica atrás do G2 e é aproveitado por dentro. **Interno.** PROPOSTA — vão esquerdo (478 mm): 4 gavetas internas (1 de acessórios + 3 de roupas), 3 prateleiras reguláveis e maleiro. Vão direito + canto (1087 mm contínuos): sapateira de 2 níveis, cabideiro longo a 1800 mm (≈ 1335 mm livres) e maleiro alto de 722 mm para malas. **Abertura.** Portas de giro embutidas (dobradiças supercurvas com amortecimento, 5 por porta) abrindo do centro; tensor embutido; puxador barra.

Nº	Peça	Qtd	Comp. × Larg. × Esp.	Material (MDF)	Fita
1	Lateral (parede do canto)	1	2520 × 544 × 15	Branco TX 15	1C
2	Lateral (lado da porta do quarto)	1	2520 × 544 × 15	Branco TX 15	1C
3	Tamponamento lateral aparente	1	2520 × 552 × 18	Carvalho claro 18	1C
4	Moldura (lado da porta do quarto)	1	2520 × 55 × 18	Carvalho claro 18	2C
5	Moldura (canto)	1	2520 × 55 × 18	Carvalho claro 18	2C
6	Base	1	1580 × 544 × 15	Branco TX 15	1C
7	Tampo	1	1580 × 544 × 15	Branco TX 15	1C
8	Divisória central	1	2490 × 544 × 15	Branco TX 15	1C
9	Divisória do canto com montante *(peça única em L: recorte de 2160 × 479 mm para a passagem das roupas)*	1	2490 × 544 × 15	Branco TX 15	1C
10	Fundo	2	2516 × 814 × 6	Branco TX 6	—
11	Frente interna da gaveta de roupas (200) *(pega usinada no topo (sem puxador saliente))*	3	445 × 200 × 18	Carvalho claro 18	2C + 2L
12	Gaveta de roupas (200): lateral	6	450 × 150 × 15	Branco TX 15	1C
13	Gaveta de roupas (200): contrafrente	3	392 × 150 × 15	Branco TX 15	1C
14	Gaveta de roupas (200): traseira	3	392 × 150 × 15	Branco TX 15	1C
15	Gaveta de roupas (200): fundo	3	450 × 422 × 6	Branco TX 6	—
16	Frente interna da gaveta de acessórios (140) *(pega usinada no topo (sem puxador saliente))*	1	445 × 140 × 18	Carvalho claro 18	2C + 2L
17	Gaveta de acessórios (140): lateral	2	450 × 95 × 15	Branco TX 15	1C
18	Gaveta de acessórios (140): contrafrente	1	392 × 95 × 15	Branco TX 15	1C
19	Gaveta de acessórios (140): traseira	1	392 × 95 × 15	Branco TX 15	1C
20	Gaveta de acessórios (140): fundo	1	450 × 422 × 6	Branco TX 6	—
21	Calço das corrediças (30 mm) *(2 chapas de 15 mm; afasta as gavetas da porta aberta)*	2	755 × 500 × 15	Branco TX 15	1C
22	Tampo do gaveteiro interno	1	530 × 478 × 15	Branco TX 15	1L
23	Prateleira regulável	3	524 × 476 × 15	Branco TX 15	1L
24	Prateleira do maleiro	1	530 × 478 × 15	Branco TX 15	1L
25	Prateleira fixa sobre a sapateira *(18 mm, apoiada na divisória do canto)*	1	1087 × 479 × 18	Branco TX 18	1C
26	Prateleira da sapateira (regulável)	1	524 × 475 × 15	Branco TX 15	1L
27	Prateleira fixa sobre o varão *(18 mm, presa também ao montante (apoio no meio do vão))*	1	1087 × 479 × 18	Branco TX 18	1C
28	Porta	2	2514 × 482 × 18	Cinza 18	2C + 2L
29	Rodapé frontal	1	1080 × 80 × 18	Cinza 18	1C
30	Rodapé lateral aparente	1	492 × 80 × 18	Cinza 18	1C


Ferragens. 10 un · Dobradiça de caneco 35 mm, supercurva, com amortecimento; 2 un · Tensor (esticador) de porta embutido; 2 un · Puxador barra reta 300 mm, alumínio ou inox escovado; 4 par · Corrediça telescópica 450 mm, extração total, com amortecimento; 16 un · Suporte de prateleira (pino metálico 5 mm); 1,087 m · Tubo cabideiro oblongo 30 × 15 mm em alumínio; 2 un · Suporte lateral para tubo cabideiro; 1 un · Suporte central para tubo cabideiro; 6 un · Pé regulável para rodapé de 80 mm, com clipe

- O canto é cego: o acesso é pela porta da direita, passando por trás do montante das dobradiças (65 mm). O varão é contínuo; as roupas do canto são as de menor uso.
- A folha da porta do quarto, aberta, fica a ≈ 26 mm da lateral deste módulo (medidas estimadas): conferir no local antes de fechar a largura de 1080 mm.
- Portas inteiras de 2514 mm (pé-direito de 2600 mm, estimado): exigem tensor e montagem no local.
- Capacidade da sapateira é pequena (≈ 6 pares à mão + espaço no canto): se precisar de mais, trocar o cabideiro longo por prateleiras ou incluir sapateira deslizante — definir.

AP Armário-ponte sobre a cama

2340 L × 1020 A × 400 P · base a 1580 do piso

Lote C1 · escala 1:10

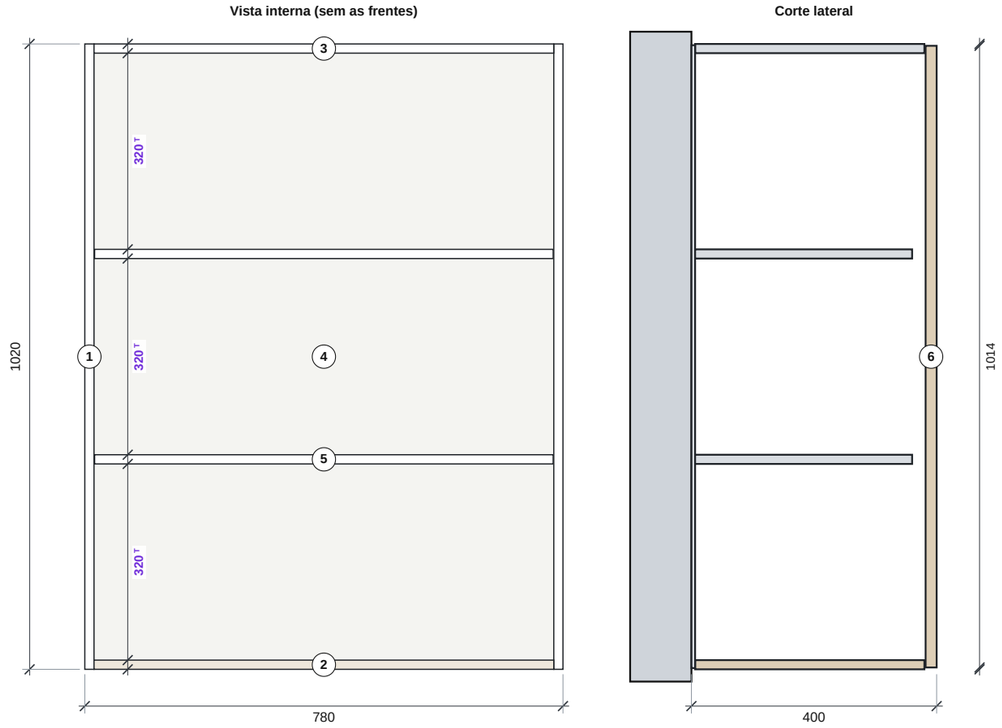

Externo. 6 portas em carvalho claro de 387 × 1014 mm, sem puxador, do topo da cabeceira ao teto. **Interno.** 3 caixas de 2 portas, 2 prateleiras reguláveis por caixa (roupa de cama, malas pequenas). Base aparente em carvalho. **Abertura.** Portas de giro em pares com fecho toque (dobradiças sem amortecedor, 3 por porta).

Nº	Peça	Qtd	Comp. × Larg. × Esp.	Material (MDF)	Fita
1	Lateral	6	1020 × 374 × 15	Branco TX 15	1C
2	Base	3	750 × 374 × 15	Carvalho claro 15	1C
3	Tampo	3	750 × 374 × 15	Branco TX 15	1C
4	Fundo	3	1016 × 776 × 6	Branco TX 6	—
5	Prateleira regulável	6	748 × 354 × 15	Branco TX 15	1C
6	Porta	6	1014 × 387 × 18	Carvalho claro 18	2C + 2L


Ferragens. 18 un · Dobradiça de caneco 35 mm, reta, sem amortecedor; 6 un · Fecho toque (pulsador); 24 un · Suporte de prateleira (pino metálico 5 mm); 6 par · Suporte de fixação de armário aéreo, regulável *(reforçado: armário sobre a cama)*

- Desenhada 1 das 3 caixas iguais. A lista traz as três.
- Altura = pé-direito − 1580 mm (1020 mm com pé-direito estimado de 2600 mm).
- Fixação estrutural na alvenaria (parede externa) com buchas adequadas e apoio no painel lateral e na coluna: armário fica sobre a cama.
- No 3D a base aparece em tom um pouco mais fechado; adotado o mesmo carvalho das portas — confirmar.

CR1 Criado suspenso 1

400 L × 100 A × 350 P · base a 420 do piso

Lote C4 · escala 1:5

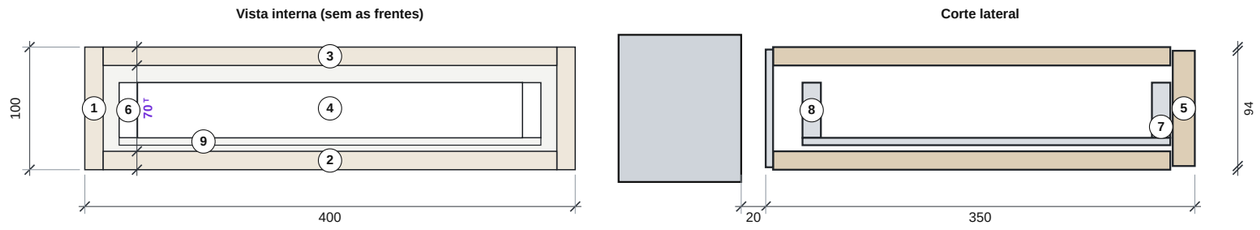

Externo. Criado suspenso em carvalho de 400 × 100 × 350 mm, a 420 mm do piso, 1 gaveta sem puxador. **Interno.** Gaveta rasa (caixa de 45 mm). **Abertura.** Corrediça telescópica de 300 mm com abertura por toque.

Nº	Peça	Qtd	Comp. × Larg. × Esp.	Material (MDF)	Fita
1	Lateral	2	324 × 100 × 15	Carvalho claro 15	1L
2	Base	1	370 × 324 × 15	Carvalho claro 15	1C
3	Tampo	1	370 × 324 × 15	Carvalho claro 15	1C
4	Fundo	1	396 × 96 × 6	Branco TX 6	—
5	Frente da gaveta *(lisa, abertura por toque)*	1	397 × 94 × 18	Carvalho claro 18	2C + 2L
6	Gaveta: lateral	2	300 × 45 × 15	Branco TX 15	1C
7	Gaveta: contrafrente	1	314 × 45 × 15	Branco TX 15	1C
8	Gaveta: traseira	1	314 × 45 × 15	Branco TX 15	1C
9	Gaveta: fundo	1	344 × 300 × 6	Branco TX 6	—

Ferragens. 1 par · Corrediça telescópica 300 mm com abertura por toque; 1 par · Suporte oculto para móvel suspenso

- São 2 criados iguais (CR1 e CR2): a lista abaixo é de uma unidade.
- Fixado sobre a cabeceira, com suporte oculto preso à alvenaria.

PJ Painel lateral da ponte (lado da janela) 30 × 2600 × 420 (L × A × P)

Lote C2

Descrição. Painel em carvalho de 30 mm (engrossado), 420 mm de profundidade, do piso ao teto.

Nº	Peça	Qtd	Comp. × Larg. × Esp.	Material (MDF)	Fita
1	Painel lateral (engrossado 30 mm) *(2 chapas de 15 mm coladas)*	2	2600 × 420 × 15	Carvalho claro 15	1C

Ferragens. 1 cj · Fixação de painel (cantoneiras, parafusos e cola PU)

- Altura = pé-direito (2600 mm, estimado).
- Fica a ≈ 148 mm do vão da janela (posição da janela estimada): conferir, inclusive o trilho/varão da cortina.

CB Cabeceira em painel 2340 × 1580 × 20 (L × A × P)

Lote C3

Descrição. 3 painéis de carvalho de 18 mm com 2 frisos verticais (juntas de 10 mm com fundo escuro), do piso à base do armário-ponte.

Nº	Peça	Qtd	Comp. × Larg. × Esp.	Material (MDF)	Fita
1	Painel da cabeceira	2	1580 × 775 × 18	Carvalho claro 18	2C + 1L
2	Painel da cabeceira	1	1580 × 770 × 18	Carvalho claro 18	2C + 1L

Ferragens. 1 cj · Fixação de painel (cantoneiras, parafusos e cola PU)

- Recortes para tomadas e interruptores da cabeceira: posições não constam na planta — levantar no local.

Imagens do modelo 3D aprovado, para comparar com os desenhos técnicos. O interior do guarda-roupa não aparece no 3D.



Parede A de frente (sem a parede do quarto 2 e sem a cama) — comparar com a elevação G-02



Guarda-roupa em L: espelho, moldura de carvalho, portas cinza e lateral



Vista a partir da janela: armário-ponte, coluna e guarda-roupa



Vista a partir da porta: cabeceira, criados e armário-ponte

DOCUMENTO	PRANCHA	ESCALA	UNIDADE	REVISÃO · DATA	FOLHA
Caderno de marcenaria Projeto executivo para orçamento	**G-10 — Suíte · imagens 3D**	**—**	**mm**	**00 · 13/11/2026**	**25/28**

Chapas de MDF (área líquida das peças)

Cor	Material	Peças	Área (m²)
	MDF 18 mm · Branco TX	5	2,28
	MDF 15 mm · Branco TX	120	32,77
	MDF 6 mm · Branco TX	28	16,73
	MDF 18 mm · Carvalho claro	22	11,99
	MDF 15 mm · Carvalho claro	13	3,64
	MDF 18 mm · Cinza	5	2,62
	MDF 18 mm · Madeira clara	9	1,59
	MDF 15 mm · Madeira clara	11	2,10
	MDF 6 mm · Madeira clara	1	0,22
	MDF 18 mm · Off-white	6	2,35
	MDF 15 mm · Off-white	4	4,61
	MDF 18 mm · Verde sálvia	20	2,85
	MDF 15 mm · Verde sálvia	3	1,35
	Total	**247**	**85,10**

Área líquida, sem perdas de corte. Para estimar chapas (2.750 × 1.840 mm ≈ 5,06 m²), acrescentar a perda do plano de corte de cada marceneiro.

Fitas de borda

Cor	Padrão	Tipo	Metros
	Branco TX	PVC 0,45 mm	91,1
	Carvalho claro	PVC 0,45 mm	4,1
	Carvalho claro	PVC 1 mm	70,4
	Cinza	PVC 1 mm	14,4
	Madeira clara	PVC 0,45 mm	9,0
	Madeira clara	PVC 1 mm	8,3
	Off-white	PVC 0,45 mm	1,3
	Off-white	PVC 1 mm	17,6
	Verde sálvia	PVC 0,45 mm	2,9
	Verde sálvia	PVC 1 mm	34,0
	Total		**253,1**

Metragem líquida das bordas indicadas nas listas de peças; acrescentar a sobra de aplicação.

Ferragens e acessórios (todos os lotes)

Item	Especificação	Qtd	Un.	Módulos
Dobradiça de caneco 35 mm, reta, com amortecimento	Porta sobreposta à lateral; aço niquelado; regulagem em 3 eixos	18	un	M4, M5, T1, G2
Dobradiça de caneco 35 mm, supercurva, com amortecimento	Porta embutida entre molduras (G4)	10	un	G4
Dobradiça de caneco 35 mm, reta, sem amortecedor	Para portas com fecho toque (o amortecedor impede a abertura por toque)	44	un	AG, AS, AM, AP
Fecho toque (pulsador)	Abertura por pressão, para portas sem puxador	17	un	AG, AS, AM, AP
Corrediça telescópica 500 mm, extração total, com amortecimento	Carga ≥ 35 kg (gavetões: ≥ 45 kg)	3	par	M1
Corrediça telescópica 450 mm, extração total, com amortecimento	Gavetas internas do guarda-roupa; carga ≥ 35 kg	4	par	G4
Corrediça telescópica 500 mm com abertura por toque	Gaveta sem puxador sob a lava-louças	1	par	M3
Corrediça telescópica 300 mm com abertura por toque	Gaveta dos criados	2	par	CR1, CR2
Perfil puxador cava em alumínio, acabamento escuro fosco	Embutido no topo de cada frente; 24 mm aparentes (como no 3D); com ponteiras	4,34	m	M1, M2, M4, M5, T1
Puxador barra reta 300 mm, alumínio ou inox escovado	Vertical; centro a 1.120 mm do piso; eixo a 40 mm da borda de abertura	4	un	G2, G4
Pé regulável para rodapé de 100 mm, com clipe	Plástico de engenharia; regulagem de ±15 mm	24	un	M1, M2, M3, M4, M5, T1
Pé regulável para rodapé de 80 mm, com clipe	Ou base em quadro de MDF nivelada — a critério do marceneiro	10	un	G2, G4
Suporte de prateleira (pino metálico 5 mm)	4 por prateleira regulável; furação a cada 32 mm	64	un	M5, AG, AS, G4, AP
Tubo cabideiro oblongo 30 × 15 mm em alumínio	Cortado na largura do vão	2,79	m	G2, G4
Suporte lateral para tubo cabideiro	Zamac ou aço, parafusado na lateral	6	un	G2, G4
Suporte central para tubo cabideiro	Preso à prateleira de cima; para vãos acima de 1.000 mm	1	un	G4
Tensor (esticador) de porta embutido	1 por porta acima de 2.000 mm, contra empeno	4	un	G2, G4
Suporte de fixação de armário aéreo, regulável	Com trilho ou bucha adequada à alvenaria; carga conforme fabricante	18	par	AG, AS, AM, NM, AP
Fixação de painel (cantoneiras, parafusos e cola PU)	Fixação oculta em piso, teto e parede	4	cj	PG, CO, PJ, CB
Suporte oculto para móvel suspenso	Preso à alvenaria, atravessando a cabeceira	2	par	CR1, CR2
Perfil de alumínio de embutir com difusor + fita de LED 2700–3000 K	Sob o aéreo de madeira, junto ao frontão	2,46	m	AM
Fonte (driver) para a fita de LED	Dimensionada pelo comprimento da fita; alojada na faixa verde	1	un	AM
Espelho prata 3 mm, bordas lapidadas	Colado em toda a face da porta; película de segurança no verso	2,17	m²	G2
Proteção da base contra umidade (manta de alumínio ou bandeja)	Nos módulos da pia e do tanque	2	un	M4, T1
Organizador de talheres para gaveta	Opcional	1	un	M1

Especificação por função, sem marca: o marceneiro informa fabricante e linha (ou equivalente técnico). Parafusos, cavilhas, minifix, buchas e cola estão incluídos na montagem. A lista por módulo está em cada prancha de detalhamento e na planilha.

Preço por lote

Lote	Descrição	Módulos	MDF m²	Valor (R$)	Observações do marceneiro
A — Cozinha					
A1	Armários de baixo da parede A (M1 a M5) e rodapé	M1, M2, M3, M4, M5, RA	13,80		
A2	Torre da geladeira (painel lateral + armário superior)	PG, AG	7,16		
A3	Aéreos (off-white, faixa verde, madeira clara e nicho do micro-ondas)	AS, FV, AM, NM	13,19		
A4	Área de serviço (módulo do tanque)	T1	2,17		
B — Guarda-roupa da suíte					
B1	Guarda-roupa de portas de espelho + coluna	CO, G2	10,77		
B2	Guarda-roupa de portas cinza + canto	G4	20,79		
C — Complementos da suíte (opcional)					
C1	Armário-ponte sobre a cama	AP	10,28		
C2	Painel lateral da ponte	PJ	2,18		
C3	Cabeceira em painel	CB	3,67		
C4	Criados suspensos (2)	CR1, CR2	1,08		
Itens opcionais e alternativas					
O1	Perfil de LED embutido sob o aéreo de madeira (2,46 m) + fonte	AM	—		
O2	Organizador de talheres na gaveta 1	M1	—		
O3	Alternativa: caixas em MDF 18 mm (todos os lotes)	—	—		
O4	Alternativa: aéreo superior com 6 portas de ≈ 512 mm	AS	—		
O5	Alternativa: cabideiro basculante no lugar do varão alto	G2	—		
Total dos lotes A e B (sem opcionais)					

Condições da proposta

Marcenaria / responsável	
Data da proposta e validade	
MDF: fabricante e linha (por padrão de cor)	
Dobradiças e corrediças: fabricante e linha	
Puxador cava: tipo e acabamento propostos	
Prazo de fabricação após a medição	
Prazo de montagem no local	
Forma de pagamento	
Garantia (estrutura, ferragens, acabamento)	
Inclui medição técnica e projeto de fabricação?	
Inclui transporte, montagem e limpeza?	
O que NÃO está incluído	
Ressalvas e pontos que mudariam o preço	

Para comparar propostas: mesmos lotes, mesmas medidas, mesmos padrões e mesmas ferragens deste caderno. Qualquer troca deve aparecer em "ressalvas".

Conferir em cada proposta

- Preço separado por lote e opcionais em linha própria.
- MDF e ferragens identificados (fabricante e linha), com amortecimento e extração total onde o caderno pede.
- Medição técnica, projeto de fabricação, transporte, montagem, réguas de ajuste e recortes incluídos.
- Prazos de fabricação e de montagem por escrito.
- Garantia por escrito e o que ela cobre.

Este caderno foi feito a partir da planta da construtora e do modelo 3D, **sem medição no local**. A tabela separa o que precisa ser medido, o que depende do modelo dos aparelhos e o que é decisão do cliente. "Muda o preço" indica o que pode alterar o valor do orçamento.

Cód.	Onde	Tipo	Pendência	Muda o preço?
P-01	Geral	medir no local	Pé-direito: não consta na planta. Adotado 2600 mm (estimado). Define a altura dos aéreos superiores (620), do painel da geladeira, do guarda-roupa (portas de 2.514), da coluna e do armário-ponte (1.020).	**sim**
P-02	Geral	medir no local	Prumo, esquadro e nível de paredes, piso e teto: levantar na medição técnica. Prever réguas de ajuste (parede e teto) em todos os encontros.	não
P-03	Geral	medir no local	Tomadas, interruptores, pontos de água, esgoto e gás existentes: não constam na planta. Levantar posição e altura de todos antes de recortar fundos, cabeceira e pedras.	não
P-04	Cozinha	medir no local	Shaft do canto (220 × 650 mm, estimado): define o início do M1, o comprimento do T1 e da pedra sob a janela (1.280 mm).	**sim**
P-05	Cozinha	medir no local	Janela da área de serviço: largura 650, peitoril 1.100 e posição estimados. Define o frontão de 200 mm e a posição da torneira do tanque.	não
P-06	Cozinha	aparelho	Modelos dos aparelhos não informados (geladeira, lava-louças, micro-ondas, lava e seca) e forno/cooktop/depurador ainda não definidos: todos os nichos usam medidas típicas. Informar marca e modelo para fechar os vãos.	**sim**
P-07	Cozinha	ponto técnico	Altura livre entre cooktop e depurador: 600 mm no projeto. Conferir o manual dos dois aparelhos (costuma ser 650 a 750 mm); pode exigir subir o aéreo de madeira ou trocar o tipo de cooktop.	não
P-08	Cozinha	decidir	Canto do L (M1 × T1): proposta de régua fixa de 40 mm + porta de 237 mm no módulo do tanque. Aprovar ou pedir alternativa ao marceneiro.	**sim**
P-09	Cozinha	decidir	Puxador cava: perfil de alumínio escuro embutido no topo de cada frente (proposto) ou cava usinada no MDF e pintada. Definir, pois muda o preço.	**sim**
P-10	Cozinha	decidir	Aéreo superior com 4 portas de 769,5 mm (desenho aprovado): largura acima do usual. Manter (3 dobradiças por porta) ou autorizar 6 portas de ≈ 512 mm.	**sim**
P-11	Cozinha	decidir	Cor do rodapé: no 3D aparece em verde mais fechado. Orçar no mesmo verde das frentes, salvo indicação em contrário.	não
P-12	Cozinha	ponto técnico	Pedras (bancadas de quartzo, frontões de granilite e revestimento do shaft) são da marmoraria — fora deste orçamento. A marcenaria precisa estar instalada antes da medição das pedras.	não
P-13	Suíte	decidir	Interior do guarda-roupa: é proposta do projeto, ainda não aprovada pelo cliente. Confirmar a divisão (cabideiro duplo no G2; gavetas, prateleiras, cabideiro longo e sapateira no G4) ou indicar o que mudar.	**sim**
P-14	Suíte	ponto técnico	Encontro das portas no canto do L: a porta direita do G2 abre contra a frente do G4. Limitar a 90° ou autorizar régua de 40 mm em carvalho no canto.	não
P-15	Suíte	medir no local	Porta do quarto: largura e posição estimadas. Aberta, a folha fica a ≈ 26 mm da lateral do G4 — conferir com a maçaneta e o batente reais.	não
P-16	Suíte	decidir	Puxador barra sobre as portas de espelho exige furar o espelho. Alternativa: perfil puxador na borda da porta. Definir.	**sim**
P-17	Suíte	medir no local	Janela da suíte (posição estimada): o painel lateral da ponte fica a ≈ 148 mm do vão. Conferir com a cortina.	não
P-18	Suíte	decidir	Cama: adotada casal padrão 1.380 × 1.880 (sugestão). Os criados de 400 mm deixam 60 mm de cada lado; se a cama for maior, os criados e a cabeceira mudam.	não
P-19	Geral	decidir	Padrões de MDF: definidos aqui por cor e descrição, sem marca. Cada marceneiro deve informar fabricante, linha e nome do padrão proposto e apresentar amostra.	**sim**

Medidas confirmadas (planta)
Cozinha: 1.500 de largura e 3.870 do shaft à parede do fundo. Suíte: 2.510 × 3.920. São cotas escritas na planta; mesmo assim, conferir na medição técnica.

Medidas estimadas
Pé-direito 2600; shaft 220 × 650; espessura das paredes; posição e tamanho de portas e janelas; fim da divisória da cozinha. Lidas pela escala da imagem da planta.

A levantar no local
Tomadas, interruptores, pontos de água, esgoto e gás; prumo e esquadro das paredes; nível do piso e do teto; rodapés e guarnições existentes.